



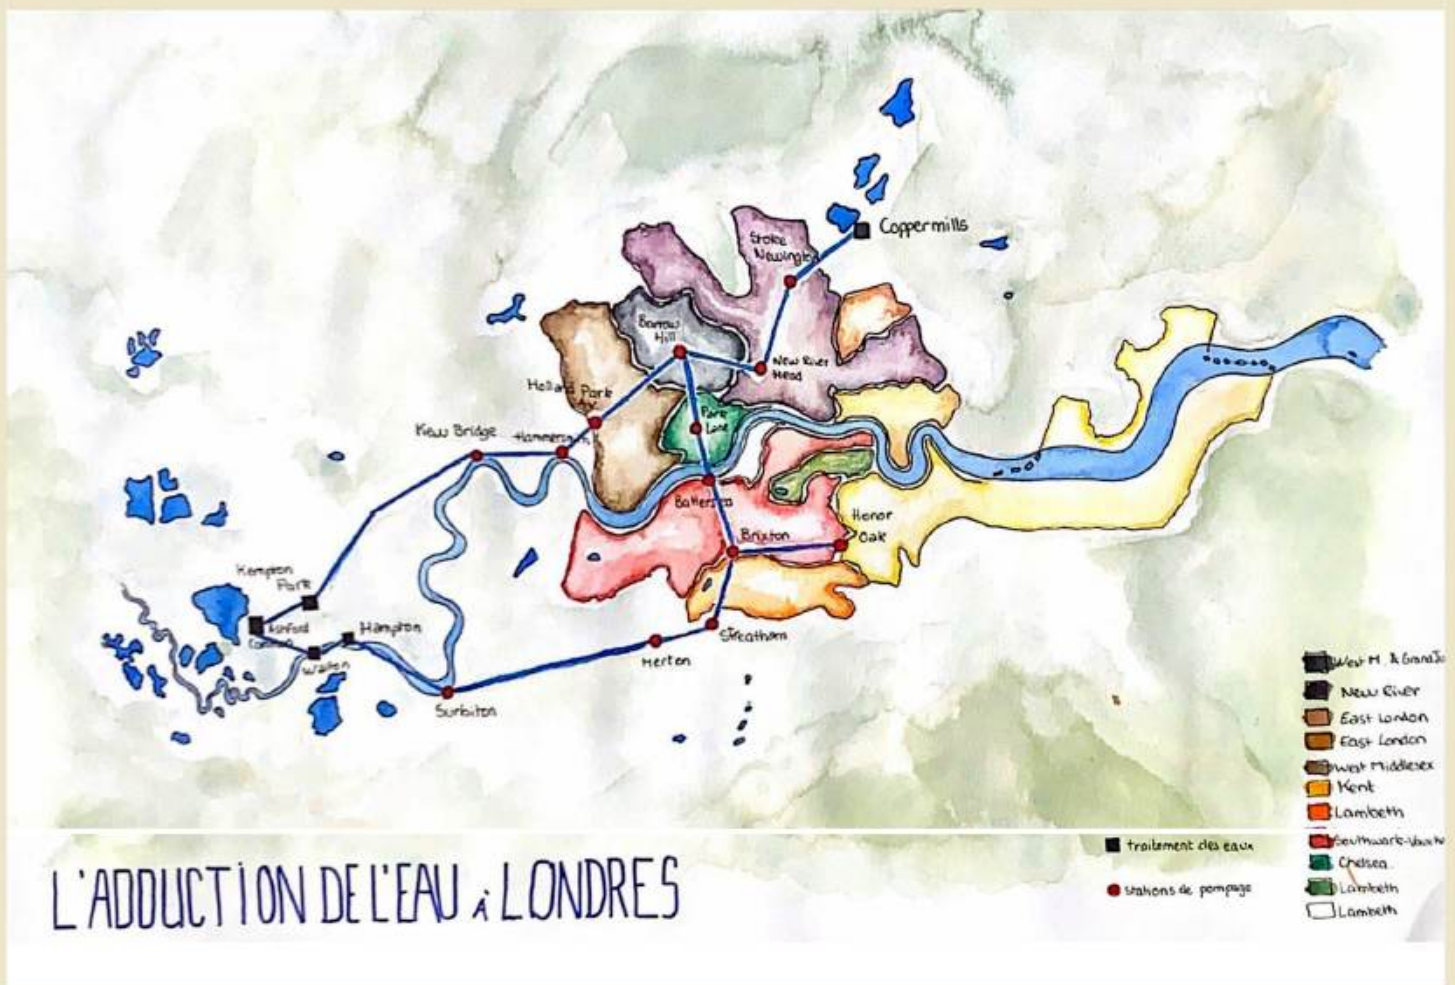

SEMESTRE 4

TECHNIQUE ET POÉTIQUE DE L'EAU
Studio Béatrice Julien

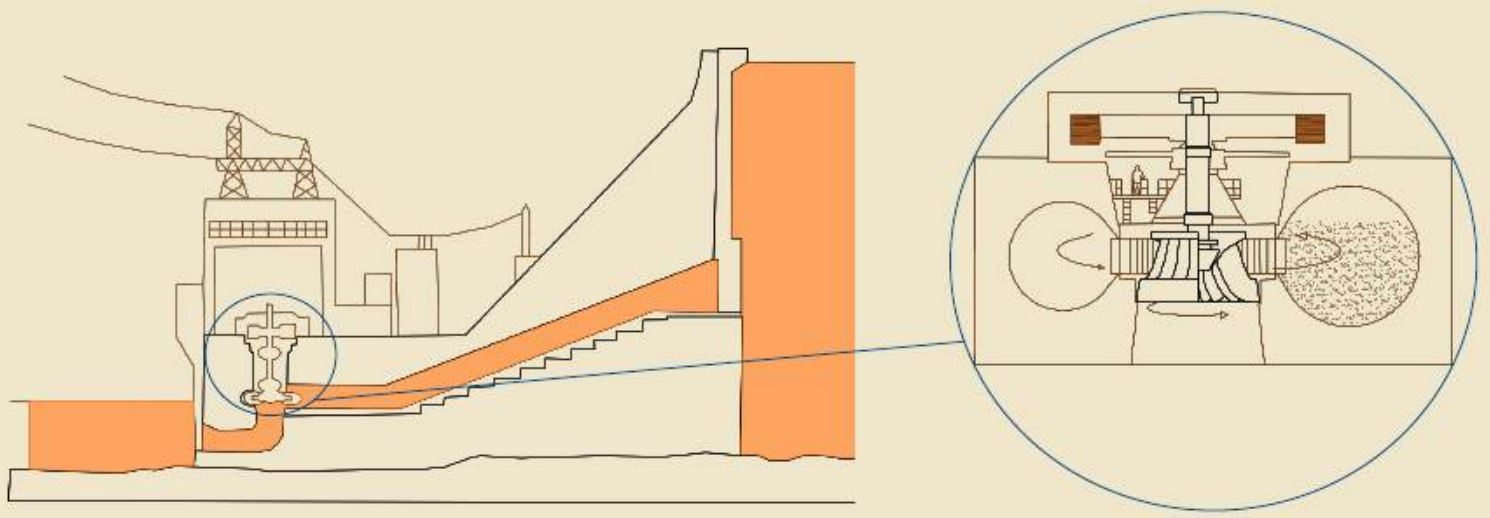

Centrale hydroélectrique, schématisation en coupe




Usine Hydraulique de Saint Maure , Élévation

SEMESTRE 4


TECHNIQUE ET POÉTIQUE DE L'EAU

Studio

Béatrice Julien

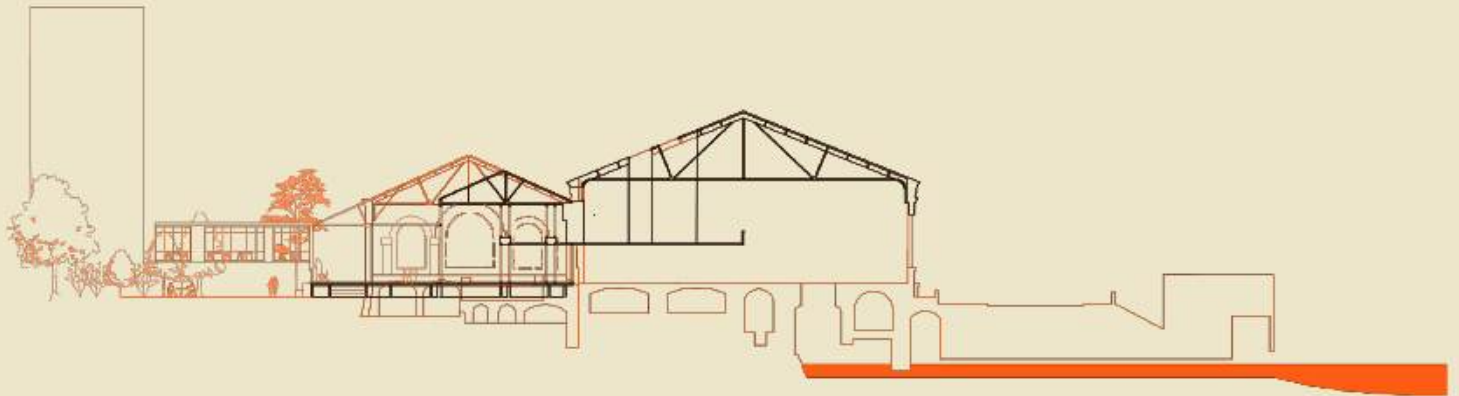

Coupe transversale AA' sur une guinguette son jardin d'hiver et les Bains/douches

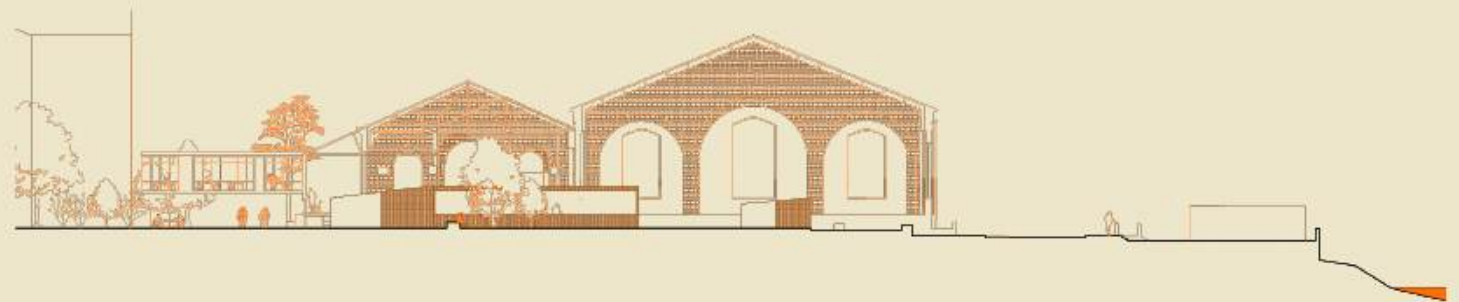

Coupe Transversale BB' sur un parc et des jardins partagés en bordure de Seine

SEMESTRE 4

TECHNIQUE ET POÉTIQUE DE L'EAU

Studio

Béatrice Julien