


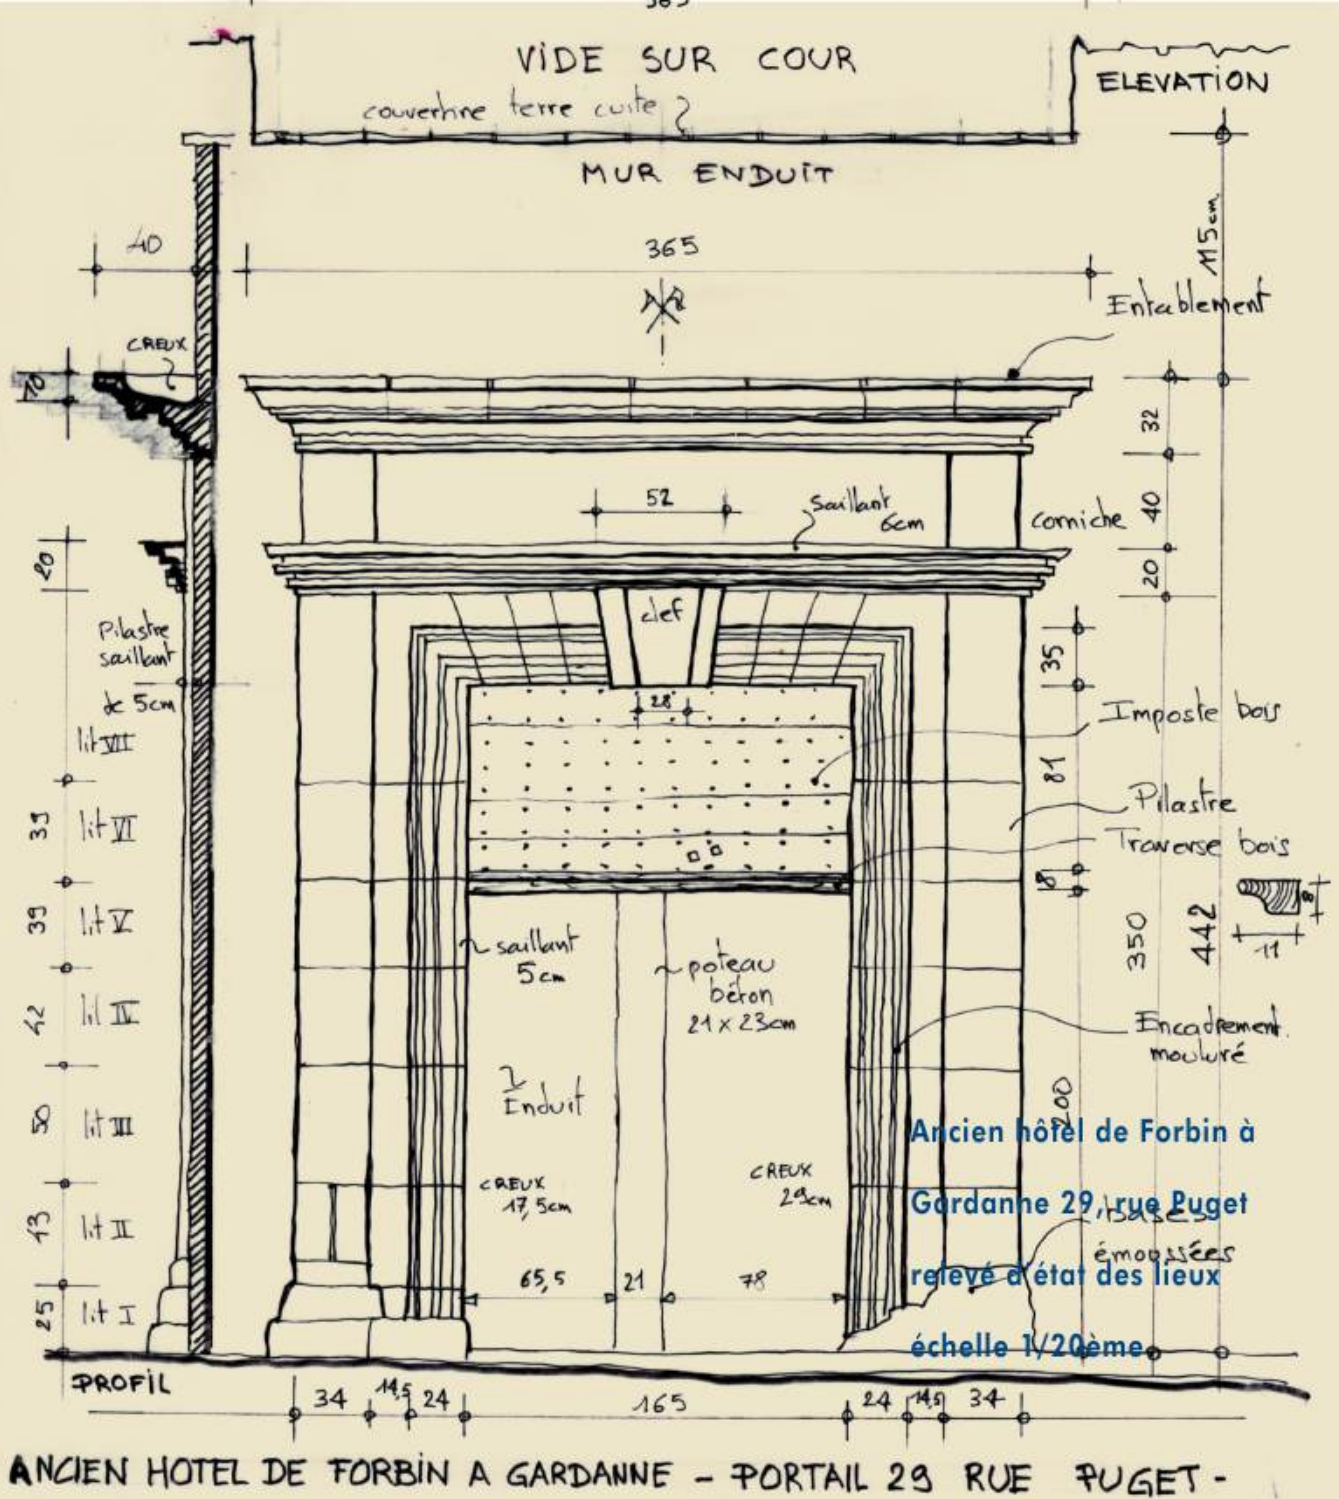

STAGE

ANIS Architecture Jérôme Durand,
Architecte du Patrimoine Juin 2023



Création d'une devanture
de magasin, 25 rue
Monclar, 13100 Aix en
Provence.

Photographie de
l'ancienne devanture d'un
CIC.

STAGE

ANIS Architecture Jérôme Durand,
Architecte du Patrimoine Juin 2023



Opération:
Creation d'une devanture
25, Rue Mondlar
13100 Aix-en-Provence

Document:
**Devanture
PROJET**

Phase:
PROJET

Maitrise d'ouvrage:
Novoid plus
4 rue des chaudronniers
13100 Aix en Provence

Date:
12/06/2023
Echelle:
1:50e

Architecte:
Jérôme Durand Architecte
1, rue Lacépède
13100 Aix-en-Provence
T 06 03 90 39 31

ANIS
Architecture

STAGE

ANIS Architecture Jérôme Durand,
Architecte du Patrimoine Juin 2023



Création d'une devanture
de magasin, 25 rue
Monclar, 13100 Aix en
Provence.

Photographie post-projet.

