

P O R T F O L I O

GABRIEL
SPARTALIOGLOU



Mon parcours en architecture s'est construit autour d'une conviction : bâtir aujourd'hui ne peut plus se penser en dehors de ce qui existe déjà les sols, les structures, les usages, les communautés. Les studios que j'ai choisis de suivre traduisent cette conviction et la prolongent, projet après projet, vers une pratique de la réhabilitation, du réemploi et de la participation.


Ces trois orientations ne sont pas des thématiques juxtaposées, mais une seule posture : celle d'un architecte qui compose avec l'existant un site, une mémoire, une communauté plutôt que d'imposer une forme close et définitive. C'est cette direction que je souhaite continuer d'explorer.




Avant-propos

1-PREMIERE ANNÉE	DU MATÉRIAU A L'ESPACE	p4
2- SEMESTRE 3	HABITER LA NAPPE	p6
Studio L2 - Pascale Richter.....		
3- SEMESTRE 4	TECHNIQUES, ET POÉTIQUE DE L'EAU DANS LA VILLE	p11
Studio L2 - Béatrice Julien.....		
4- SEMESTRE 5	TRANSFORMER, AGIR AVEC CE QUI EST LA.	p14
Studio L3 - Mirabelle Croizier.....		
5- SEMESTRE 6	RÉINVENTER L'EXISTANT	p23
Studio L3 - Vanessa Fernandez participation concours 2024.....		
6- SEMESTRE 7/8	LABORATOIRE DE RESTAURATION	p29
Studio M1 - Daniela Esposito et Valeria Montanari - LA SAPIENZA à Rome.....		
7- SEMESTRE 9	JARDIN PERMACULTUREL	p34
Studio M2 - Philippe Vilien.....		
5- STAGE PREMIÈRE PRATIQUE Juin 2023		
Jérôme Durand, architecte du patrimoine.....;		p37
6- ARTS PLASTIQUES	RÉALISATIONS PERSONNELLES	p41

Sommaire

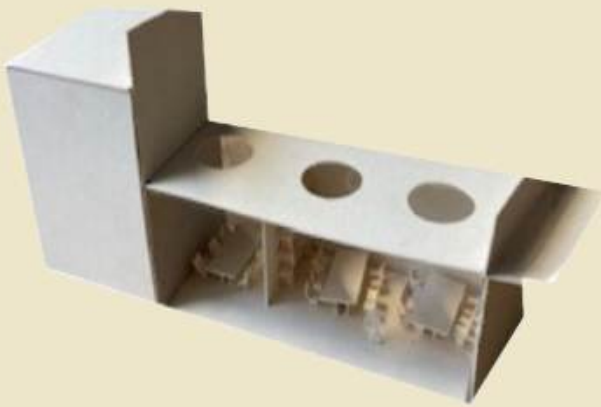

1

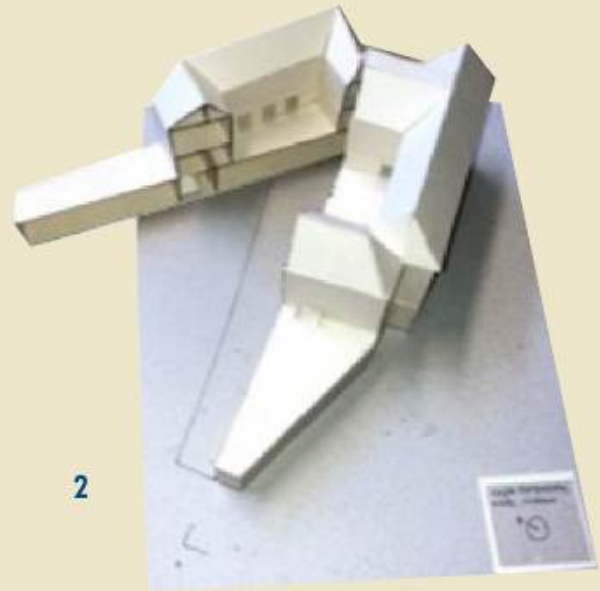


2

Voici trois maquettes d'analyse Faculté de droit d'Urbino représentant respectivement, La bibliothèque sous-sol (1), le bâtiment dans son ensemble (2), sa relation avec le paysage (3).

Voyage d'étude en Italie, ville d'Urbino.
Nous avons analysé la faculté de droit en prenant comme axes directeurs la topographie du Site, la relation entre le bâti et les espaces publics des alentours. Ce projet d'analyse a débuté à Paris puis s'est prolongé in situ. Les visites de différents complexes universitaires, places et même palais ont enrichis ma capacité à prendre des relevés, observer. En effet, formuler des hypothèses ou tirer des conclusions ont joué un rôle primordial tout au long de ce voyage.

Avoir la chance de visiter et rentrer en contact avec des œuvres marquantes de la carrière d'un architecte tel que Giancarlo di Carlo dès le premier semestre du cursus fût un tournant dans mon parcours.

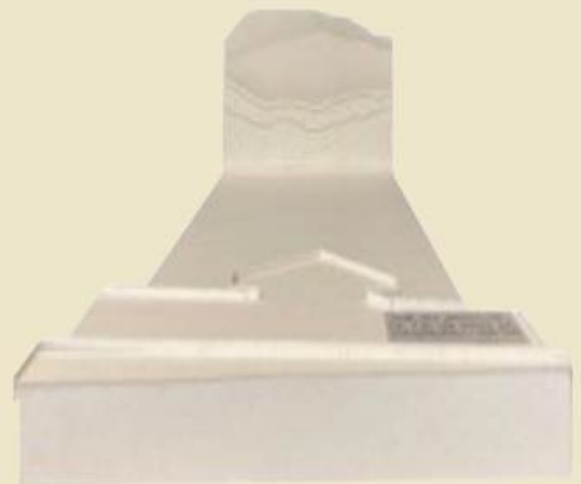

3

SEMESTRE 1


DU MATÉRIAU A L'ESPACE



Maquette d'un atelier/logement 80, rue de Ménilmontant, 75020

SEMESTRE 2

USAGES D'UN LIEU

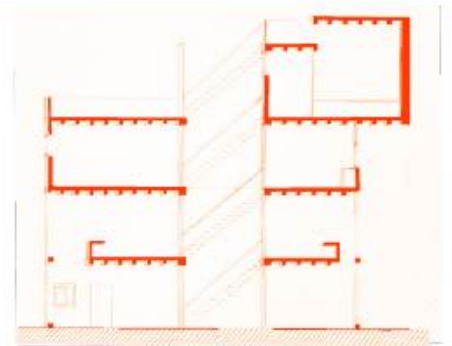

coupe d'un atelier/logement



Axonométrie montrant le
système d'assemblage
des unités d'habitation
(murs mitoyens en redans)

SEMESTRE 3

HABITER LA NAPPE, studio Pascale Richter

Vaujours — 88 logements intermédiaires

Le projet naît de la lecture d'un tissage : alternance de pleins et de vides, porosité centrale, longues lignes verticales, redans et décalages. De cette trame découle un principe d'étirement spatial, le logement en longueur mis en dialogue avec des ouvertures qui le traversent.

Sur un terrain accolé à la forêt, le projet densifie le tissu existant sans rompre avec lui: seul étage, à la hauteur des habitations voisines. Une même unité se démultiplie 88 fois

par murs mitoyens et forme une nappe de trois bandes en quinconce. La forêt s'avance dans les interstices, protège la bande sud des nuisances de la départementale et limite les vues entre les bandes nord et centrale.

Chaque T3 de 106 m² s'organise autour de deux espaces extérieurs reliés en diagonale; un puits de lumière au-dessus de l'escalier laisse glisser la lumière jusqu'à la cuisine. L'espace de travail se convertit en chambre selon les besoins. À l'avant, les jardins font office d'accès et d'espaces capables, ouverts à une extension future.



Les accès se font par des venelles. Une venelle centrale relie deux espaces communs contrastés : une placette minéralisée, et un second que la forêt vient déborder.

SEMESTRE 3


H A B I T E R L A N A P P E , s t u d i o P a s c a l e R i c h t e r



Tissage personnel, point de départ du projet.

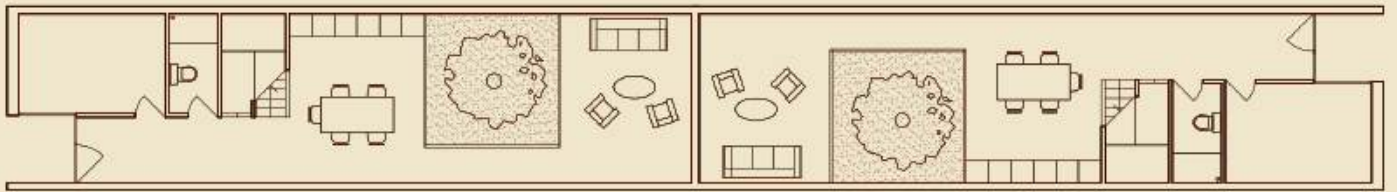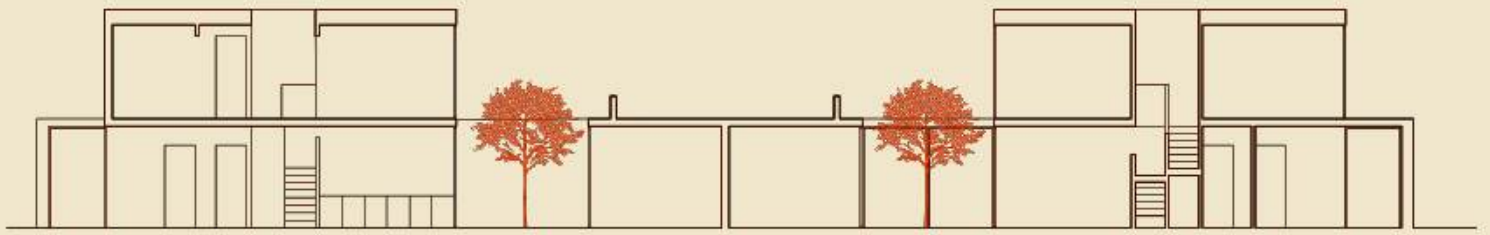

SERVIR L'ENSEMBLE

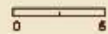


Plans et Coupe
Longitudinale sur une
unité d'habitation
dupliquée en miroir.

SEMESTRE 3

HABITER LA NAPPE, studio Pascale Richter




Maquette d'assemblage au 1/200eme, système de murs mitoyens.

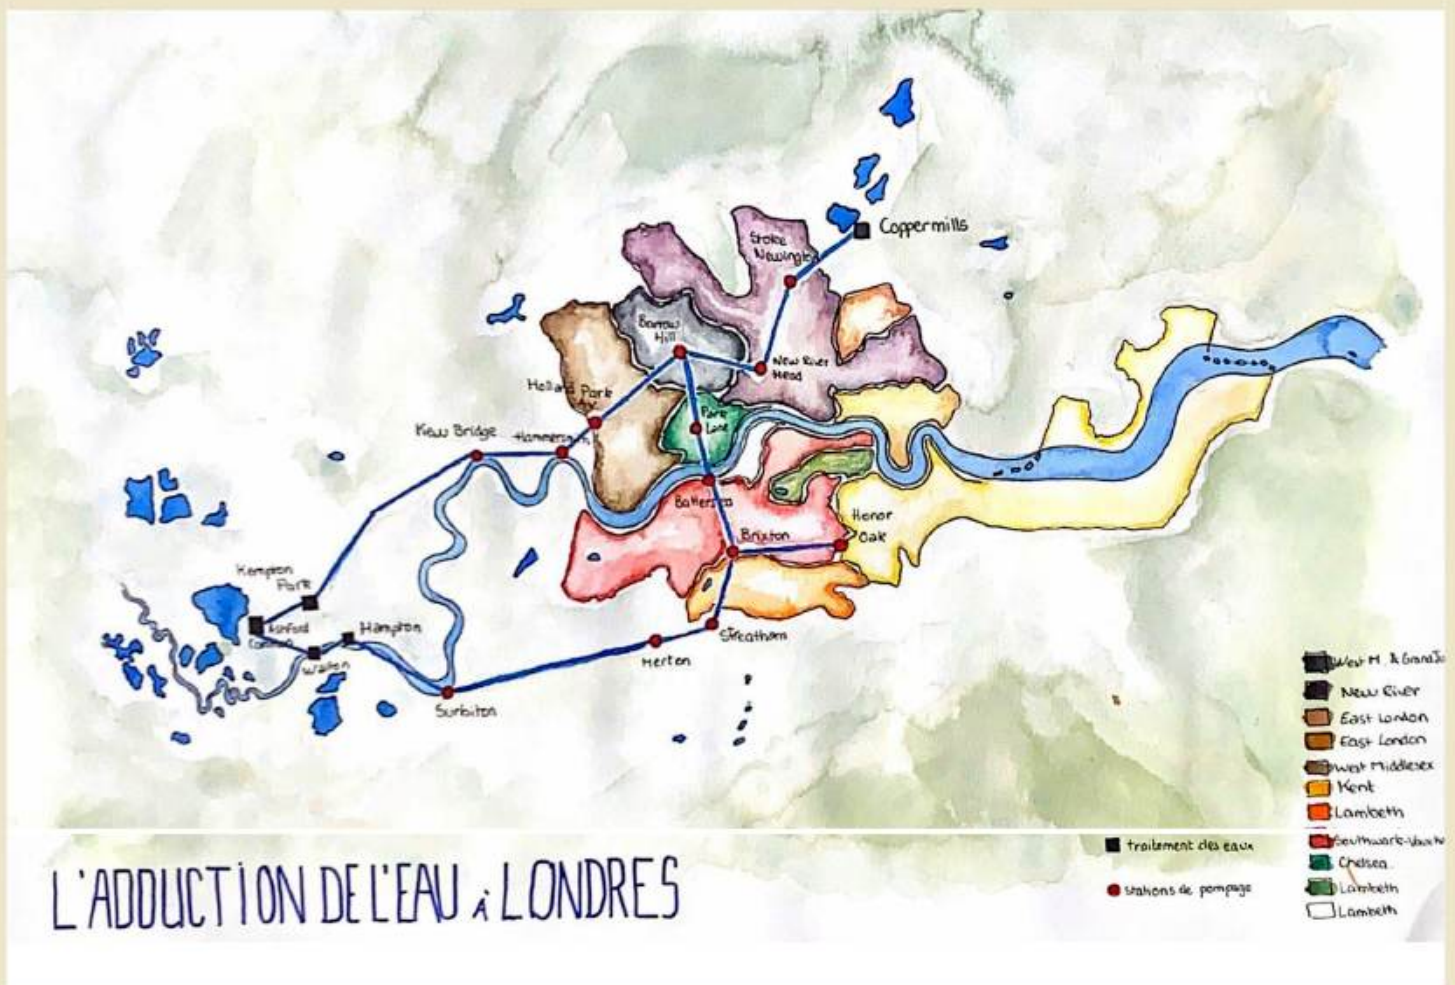

SEMESTRE 4

TECHNIQUE ET POÉTIQUE DE L'EAU
Studio Béatrice Julien

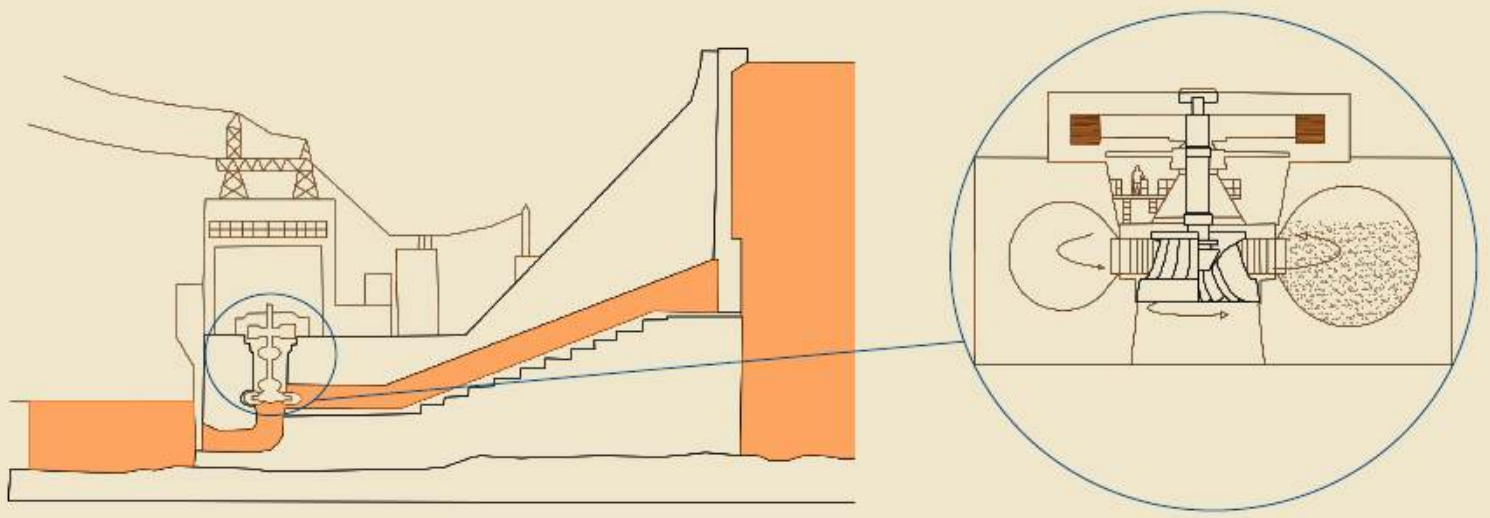

Centrale hydroélectrique, schématisation en coupe




Usine Hydraulique de Saint Maure , Élévation

SEMESTRE 4


TECHNIQUE ET POÉTIQUE DE L'EAU

Studio

Béatrice Julien

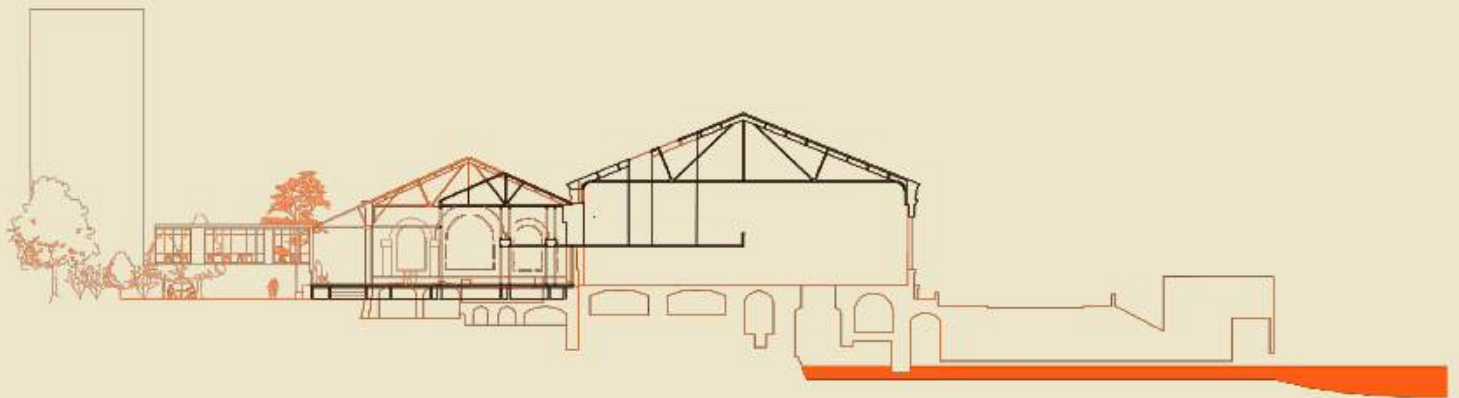

Coupe transversale AA' sur une guinguette son jardin d'hiver et les Bains/douches

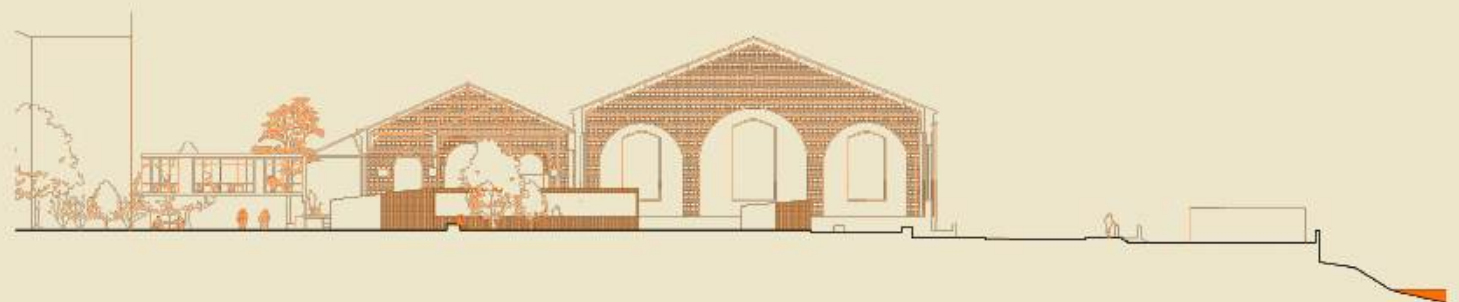

Coupe Transversale BB' sur un parc et des jardins partagés en bordure de Seine

SEMESTRE 4

TECHNIQUE ET POÉTIQUE DE L'EAU

Studio


Béatrice Julien



Ferme de la Croix Blanche, Lavis

SEMESTRE 5

TRANSFORMER, AGIR AVEC CE QUI
EST LA, studio Mirabelle Croizier

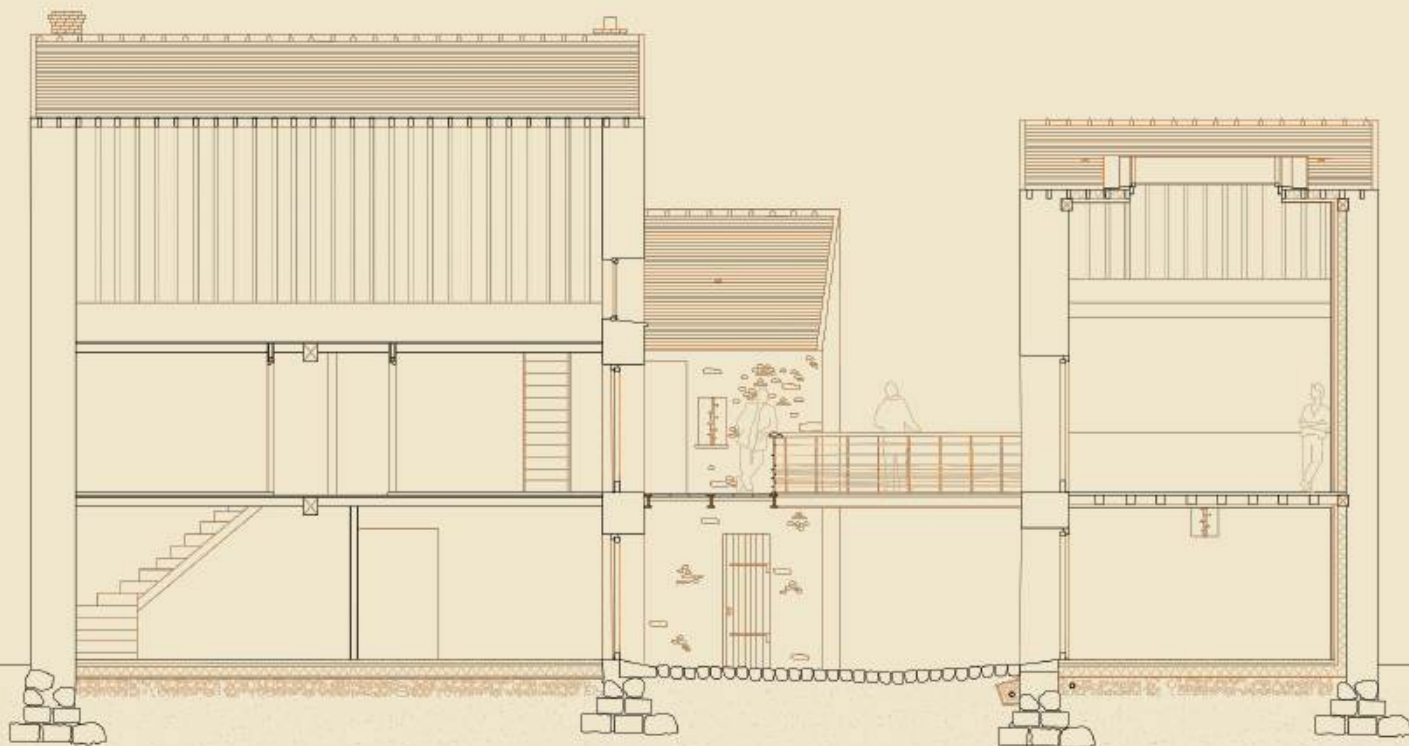

coupe transversale FF'




Coupe sur préau



SEMESTRE 5

TRANSFORMER, AGIR AVEC CE QUI
EST LA

studio Mirabelle Croizier

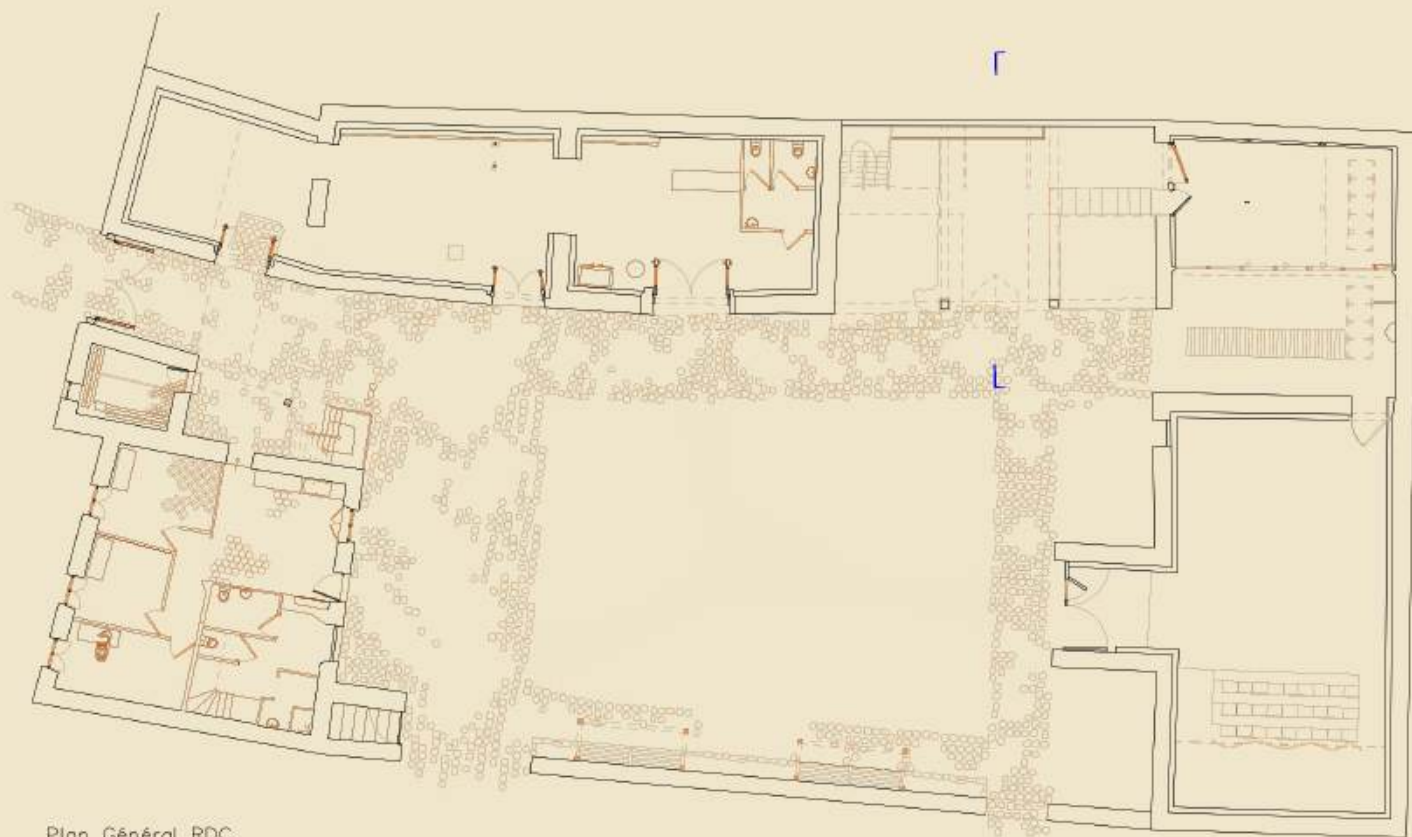

Plan Général RDC

0 2 10m






Marianne Paysagiste

Solange
Accompagnatrice

Maire de Blandy-les-Tours

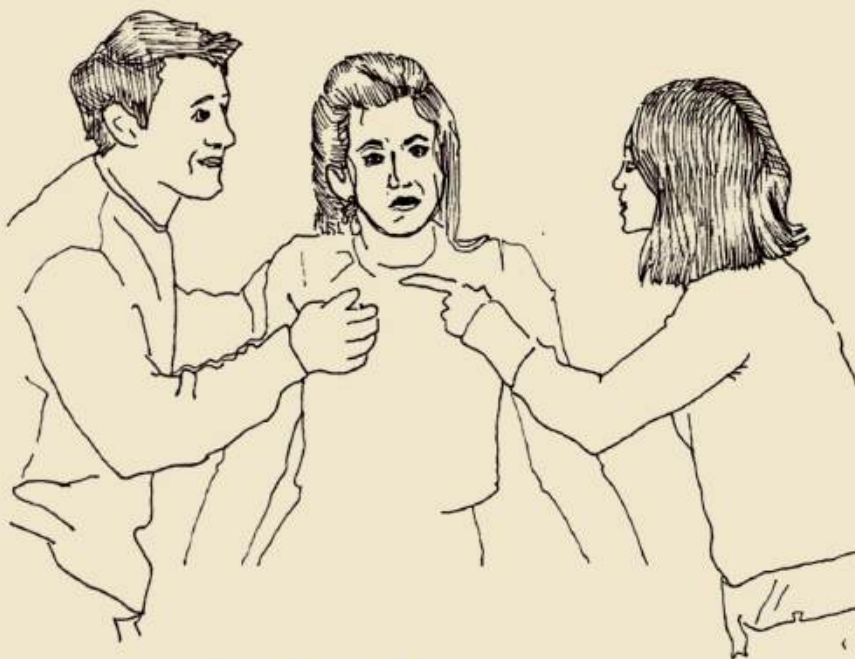


Les Touristes

SEMESTRE 5

TRANSFORMER, AGIR AVEC CE QUI
EST LA

studio Mirabelle Croizier

Agriculteurs

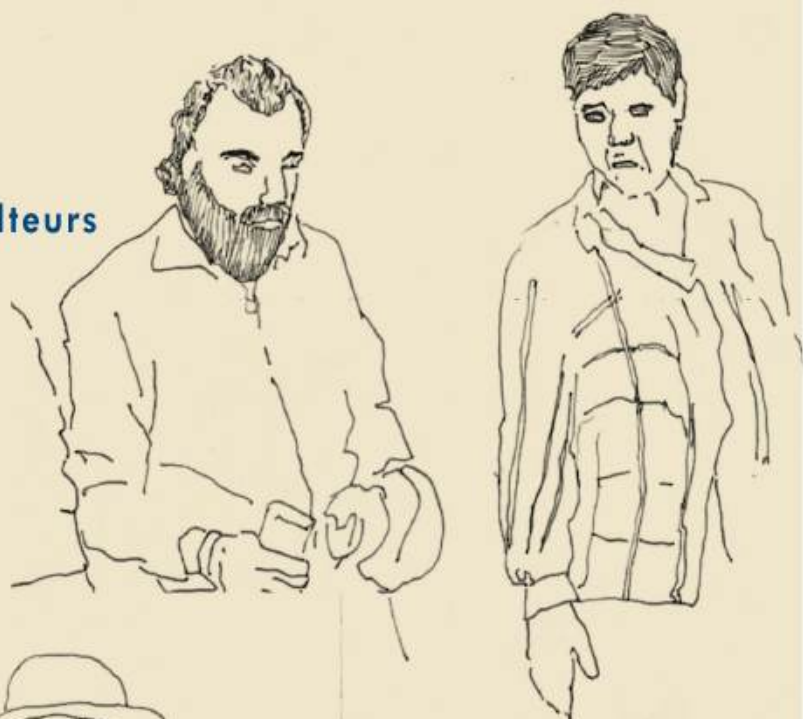

Les résidents

Musicien·nes et acteur·ices





**Présidente du
conseil associatif**



Axonométrie éclatée et dessinée ordinateur et crayon sur papier. Représentant par un fil rouge la déambulation dans le projet.

Le document d'origine sur format A0 est accompagné de croquis des vues proposées coresspondants aux personnages de l'axonométrie générale. Ci dessous les deux premières vues.

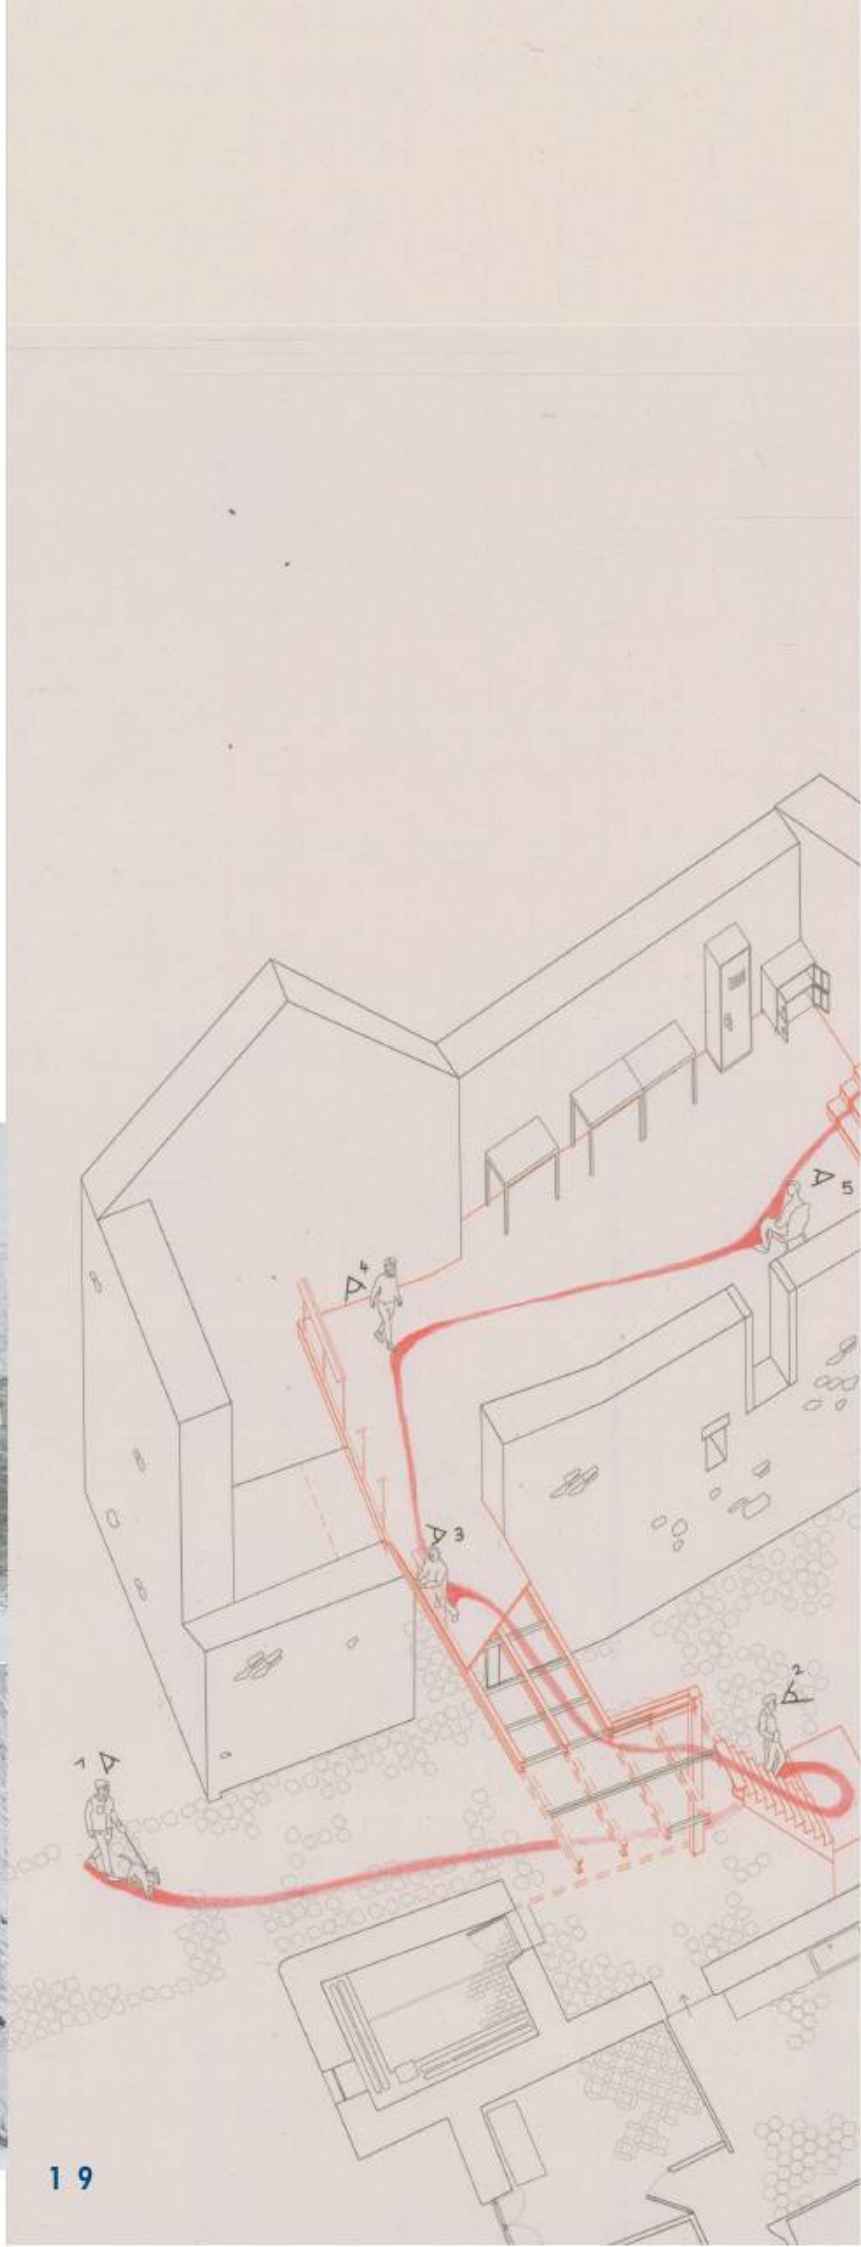

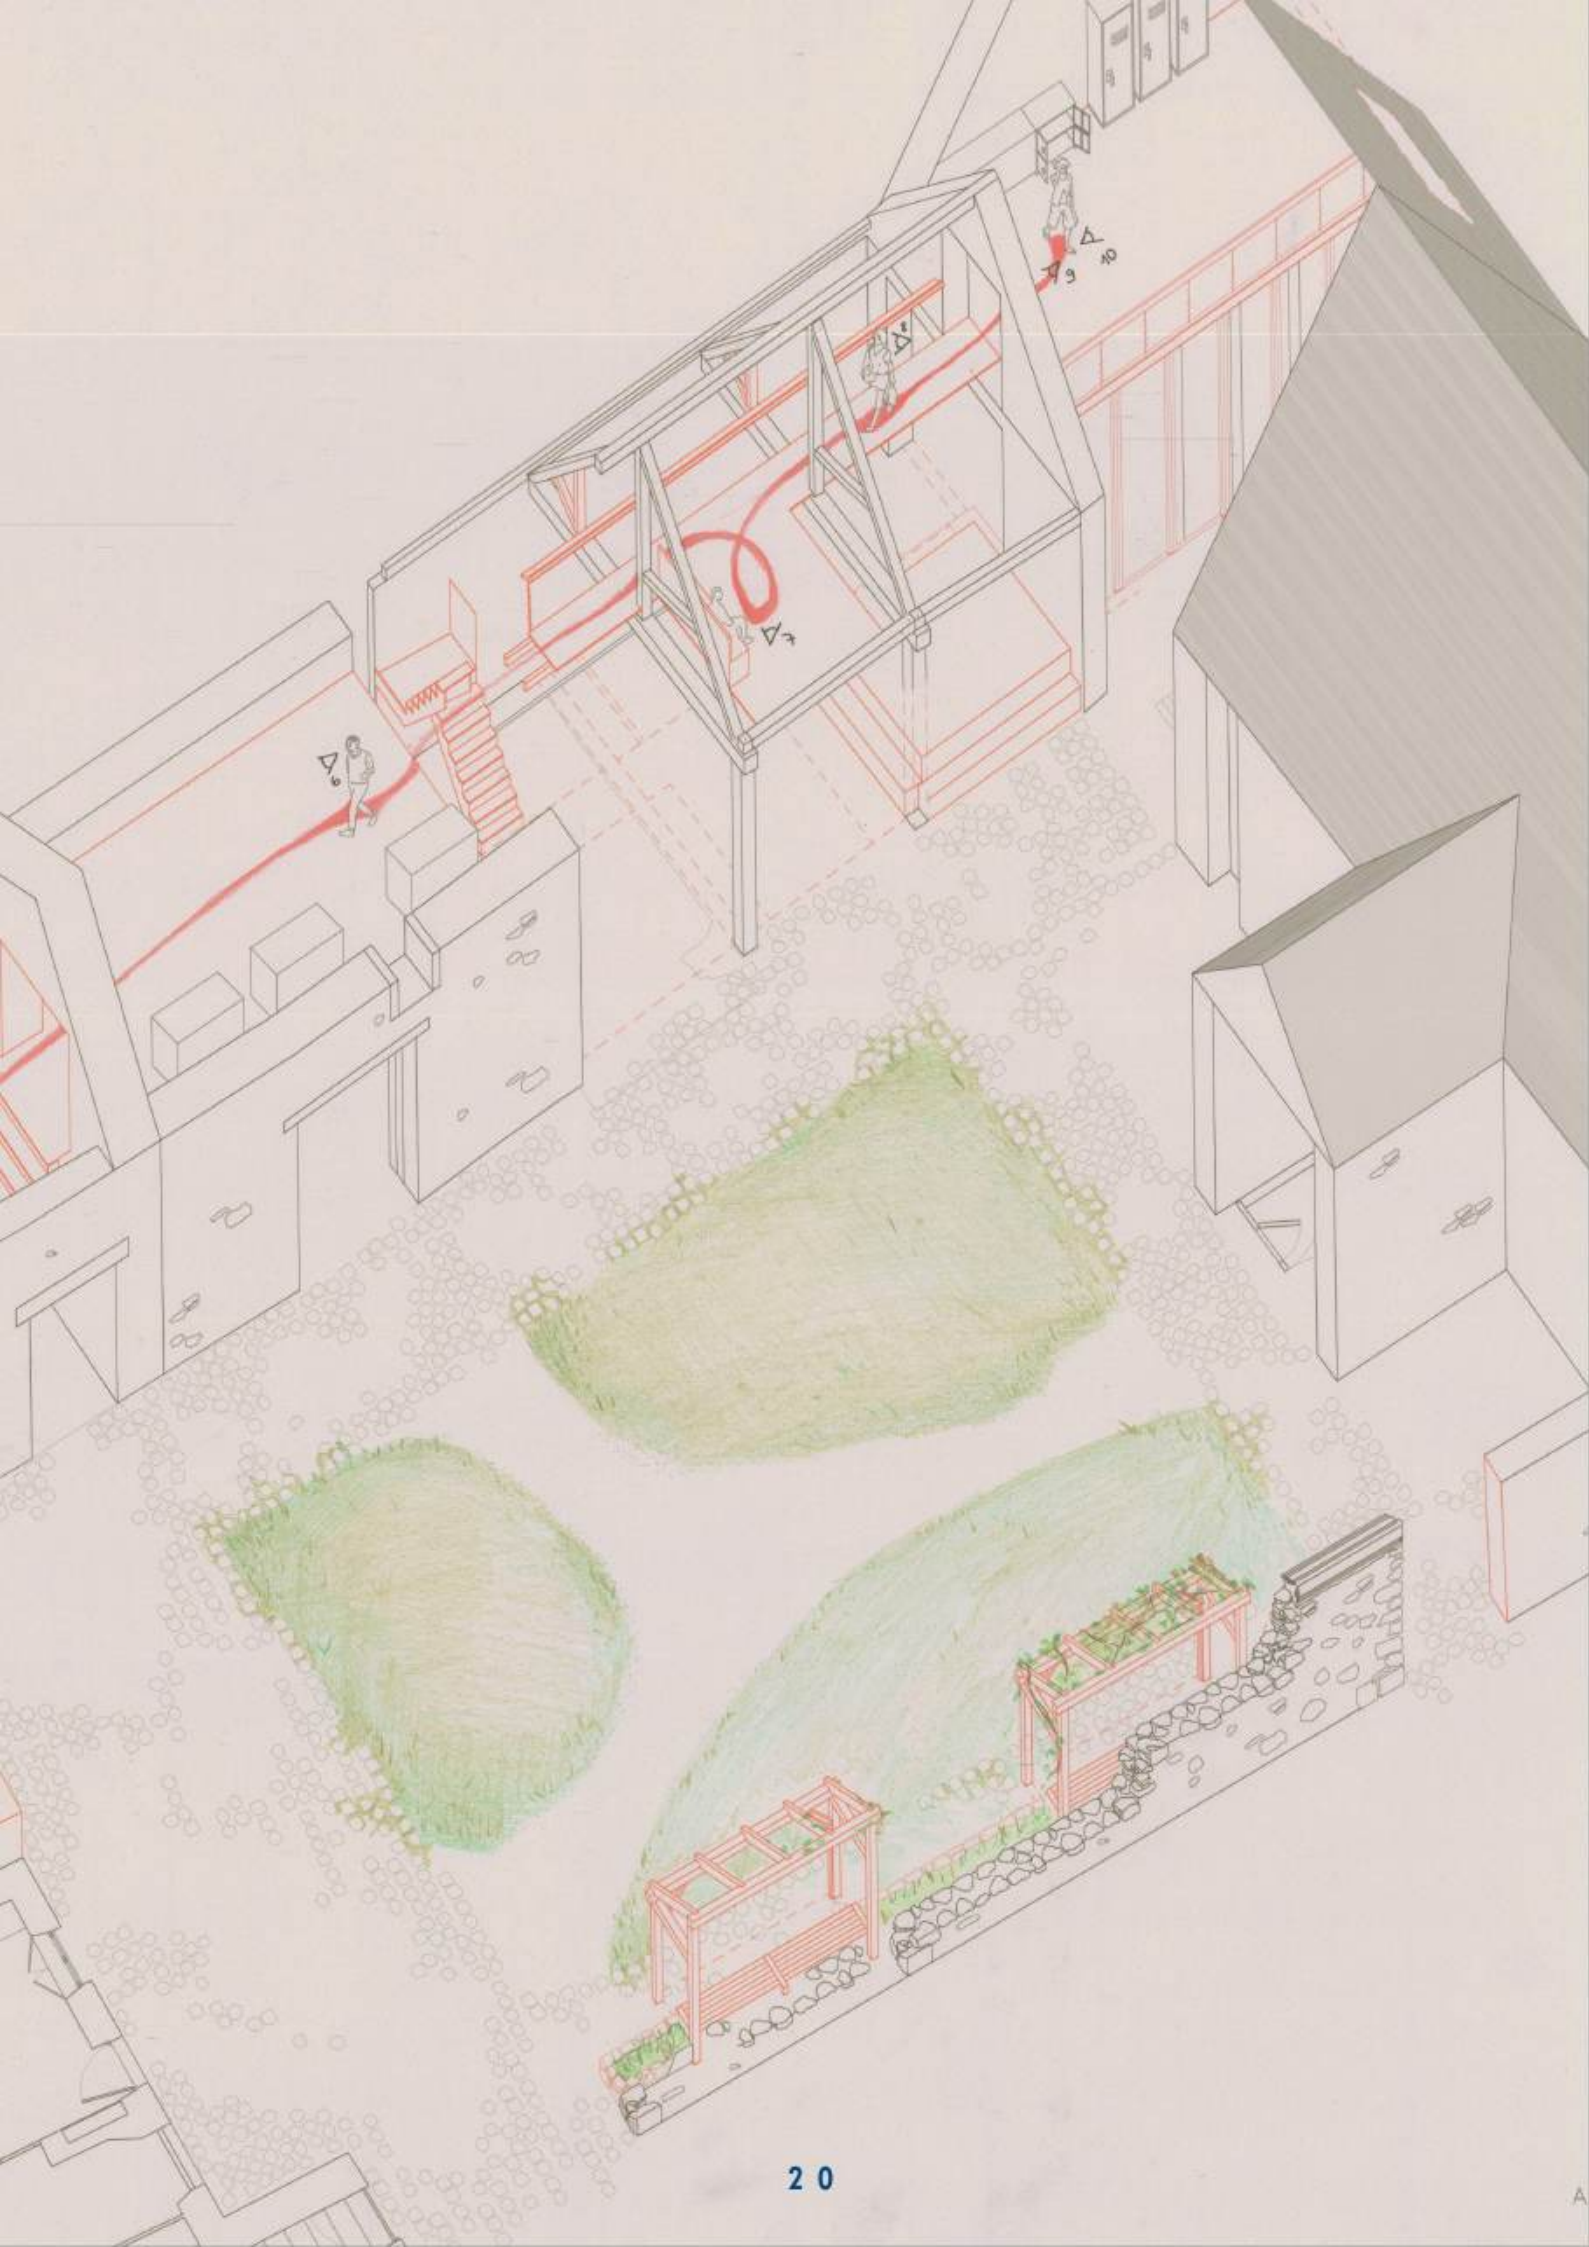



3 - passerelle d'entrée



8 - passerelle dans la charpente



5 - salle des associations



7 - mezzanine dans la charpente

LA BALADE DANS LA FERME

La réhabilitation de l'ancienne ferme de la Croix Blanche articule une succession de programmes le long d'un même parcours. Une galerie d'exposition mène à la billetterie-boutique du musée, puis à un préau accueillant des ateliers participatifs autour des arts plastiques et de la botanique.

Au cœur de la charpente conservée, une passerelle à l'écriture contemporaine distribue les ateliers d'artistes de l'étage, dont un plancher réservé à l'association des Mémoires de Blandy. Une seconde passerelle referme la boucle vers l'ancienne maison, ménageant au passage des vues croisées sur les œuvres et le bâti existant grâce au jeu des doubles hauteurs.

En fond de parcelle, un bâtiment accueille séminaires, conférences et répétitions des événements médiévaux. L'ancienne maison, elle, réunit bureaux du château, sanitaires, chambres et dortoir sous les combles.


LA BALADE DE LA FERME

À Blandy-les-Tours, la balade se greffe à la randonnée des trois châteaux et aux vélo-routes qui traversent la commune. Paysagée avec les essences typiques du plateau de la Brie, elle forme une boucle reliant la ferme, l'antenne du jardin d'Hygie et le château. Une succession d'interventions paysagères légères marque les points remarquables, géologiques ou historiques, où des cartels renseignent le visiteur sur l'histoire du lieu, son sous-sol et les vertus des essences plantées.

SEMESTRE 5

TRANSFORMER, AGIR AVEC CE QUI
EST LA

studio Mirabelle Croizier

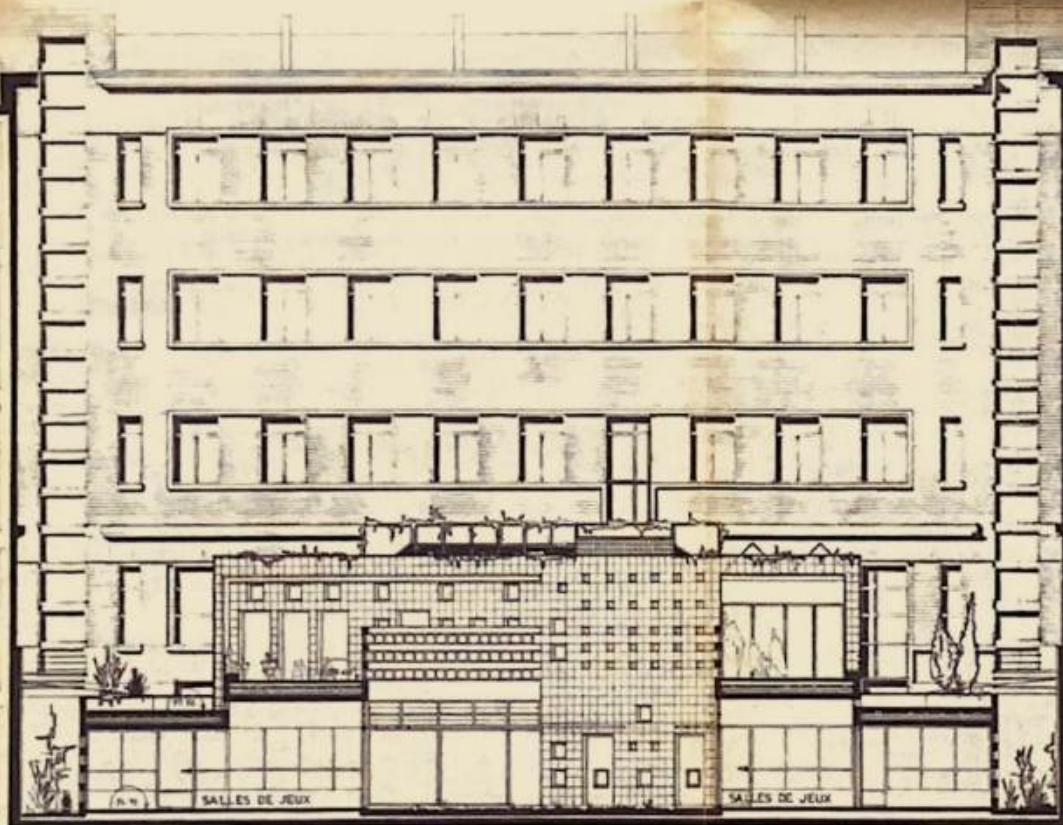

COUPE TRANSVERSALE

4 JUIN 1985

ASSISTANCE PUBLIQUE HOPITAUX DE PARIS
DIRECTION DES EQUIPEMENTS 3, AVENUE VICTORIA PARIS 10^e

HOPITAL ST VINCENT DE PAUL
74 AVENUE DENFERT ROCHEREAU 75 014 PARIS
CRÈCHE DES ENFANTS DU PERSONNEL

SEMESTRE 6

RÉINVENTER L'EXISTANT

Studio Vanessa Fernandez

URGENCE ÉTUDIANTE :
**UNE RÉSIDENCE
A PRESCRIRE!**

Il s'agit de la réhabilitation d'un
Hôpital abandonné en résidence
étudiante. Le site étant au choix,
Nous avons proposé de partir du
contre-projet pour aller vers
la résidence CROUS de rêve...

6750 Logements étudiants
disponibles à Paris Intra-muros

Entre **30000** et **60000**
demandes chaque année.

Le quartier de Saint Vincent de Paul
à retenu notre attention. Paris métropole
Et aménagements a entamé un projet
d'éco-quartier en 2017. La livraison des
Derniers bâtiments est annoncée pour
2029.

SEMESTRE 6

RÉINVENTER L'EXISTANT

Studio

Vanessa Fernandez

T6

Superficie : 118 m²



Nous avons cherché à dépasser la réponse standardisée du logement étudiant où une cellule se repète à l'identique pour proposer une pluralité d'habiter. Seize typologies différentes ont ainsi été imaginées, du T1 au T6, déclinées en studios individuels ou en colocations.

Cette diversité typologique répond à la diversité réelle des profils étudiants : premières années en quête d'un cocon minimal, doctorants ayant besoin d'un espace de travail dédié, groupes d'amis souhaitant partager un T5 ou un T6 avec cuisine et séjour communs. Plutôt qu'une résidence uniforme reproduisant la même cellule sur plusieurs étages, chaque typologie devient une réponse spécifique à un mode de vie, une durée de séjour, une manière d'habiter seul ou à plusieurs.

T5

Superficie : 91 m²



T1


Superficie : 20 m²




SEMESTRE 6

RÉINVENTER L'EXISTANT

Studio Vanessa Fernandez

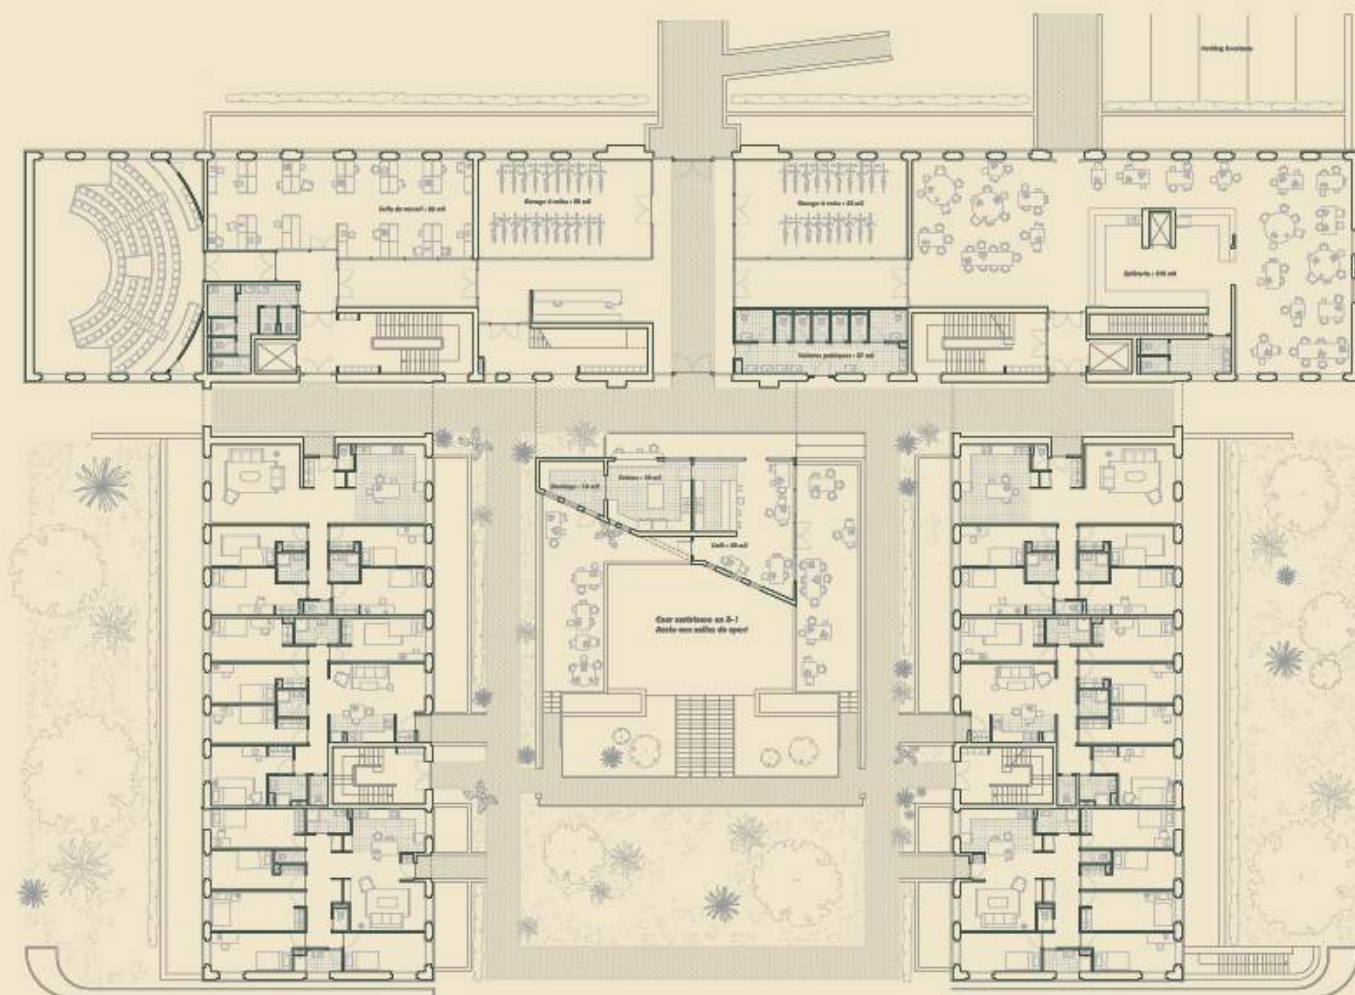

Le rez-de-chaussée de la résidence s'ouvre largement sur le quartier et accueille les programmes partagés entre les étudiants et les habitants du futur éco-quartier : une médiathèque, un café, un amphithéâtre, des studios de musique ainsi que des salles de danse et ateliers d'arts. Ce socle actif prolonge la vie de la résidence au-delà du Seul logement, en offrant des espaces de pratique et de rencontre qui irriguent le quartier bien au-delà des horaires étudiants.

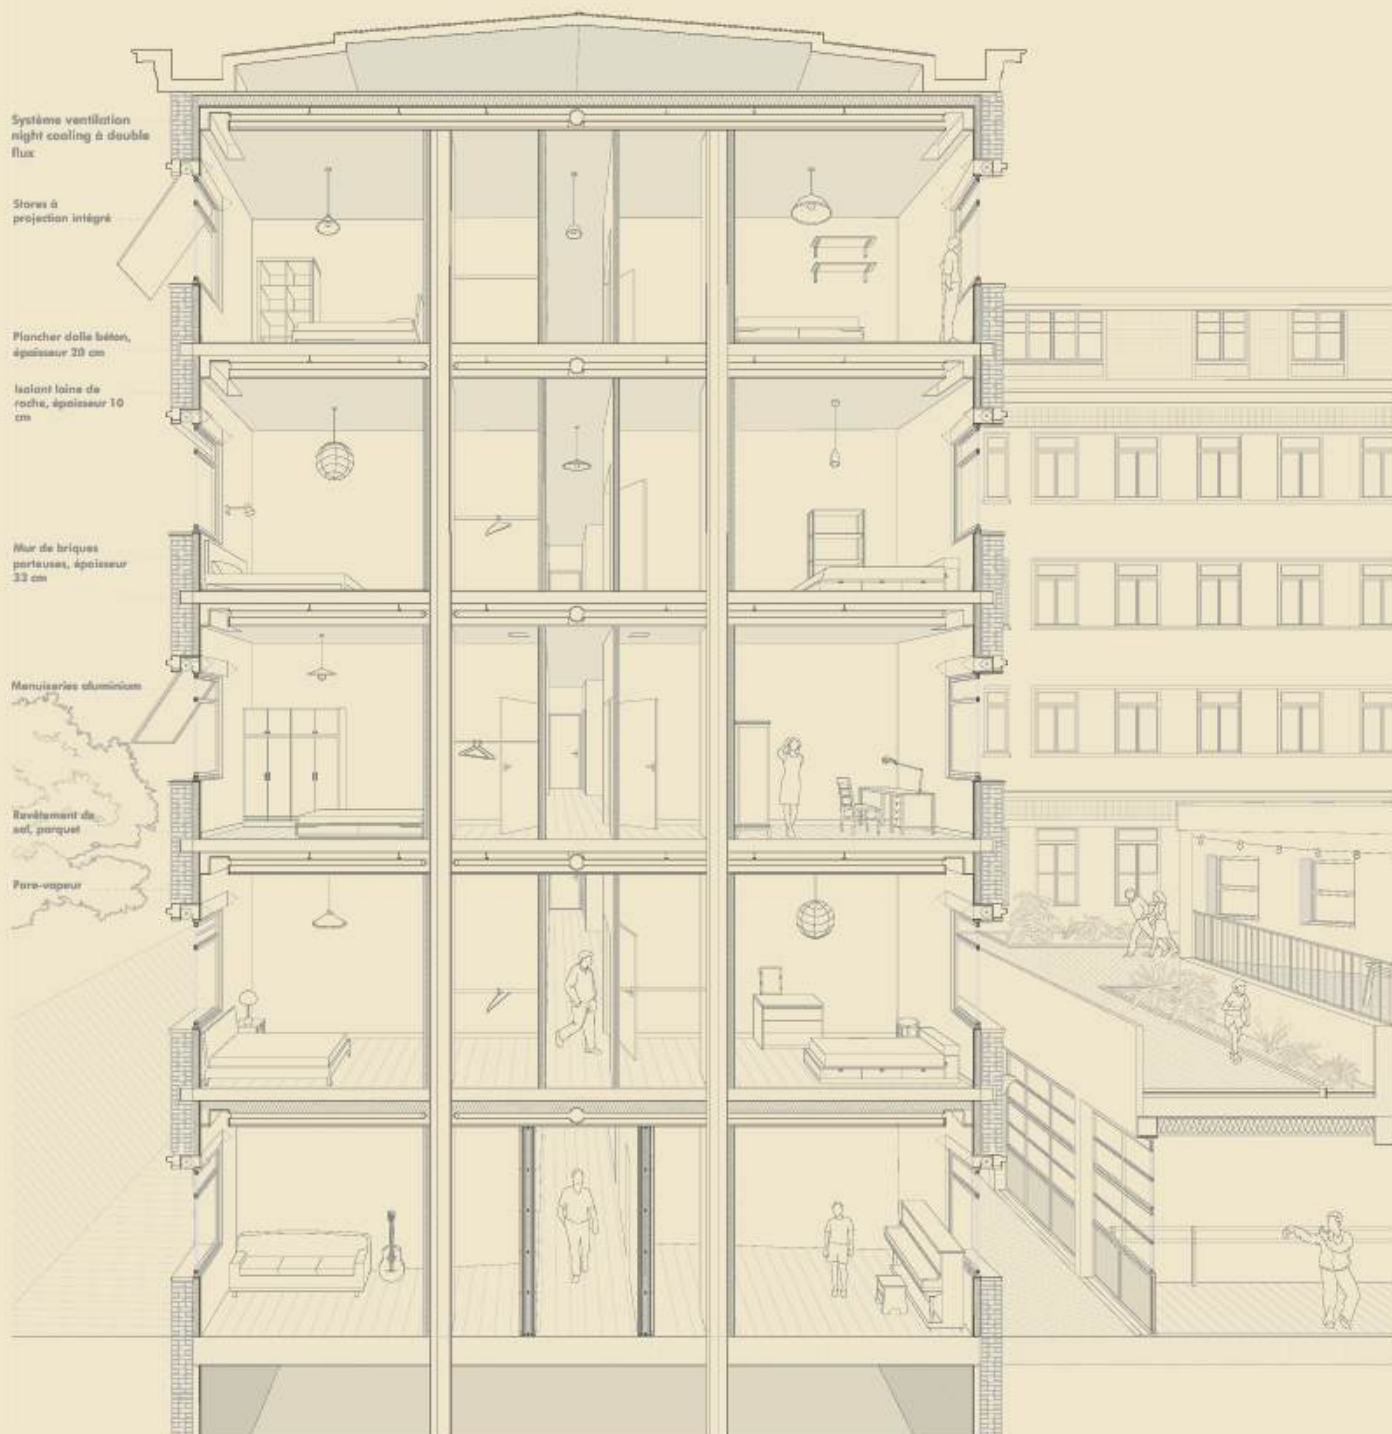

0

SEMESTRE 6

RÉINVENTER L'EXISTANT

Studio Vanessa Fernandez

SEMESTRES 7et8


LABORATORIO DI RESTAURO

Studio Daniela Esposito, Valeria Montanari

UNIVERSITA LA SAPIENZA, ROMA


Proporzioni della fase antica, pianta

Fonte: Elaborazione dell'autore

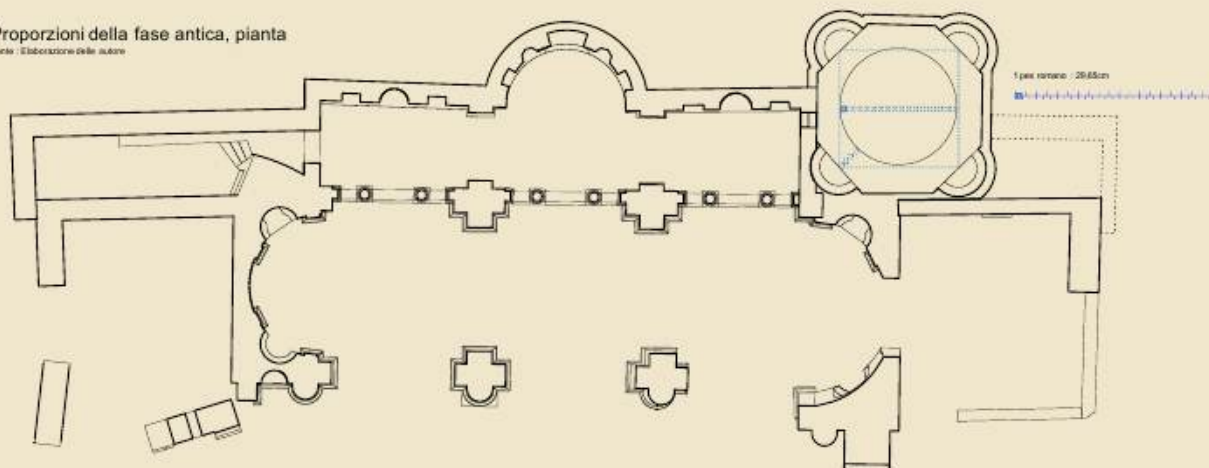


Proporzioni della fase del Bramante, pianta

Fonte: Elaborazione dell'autore

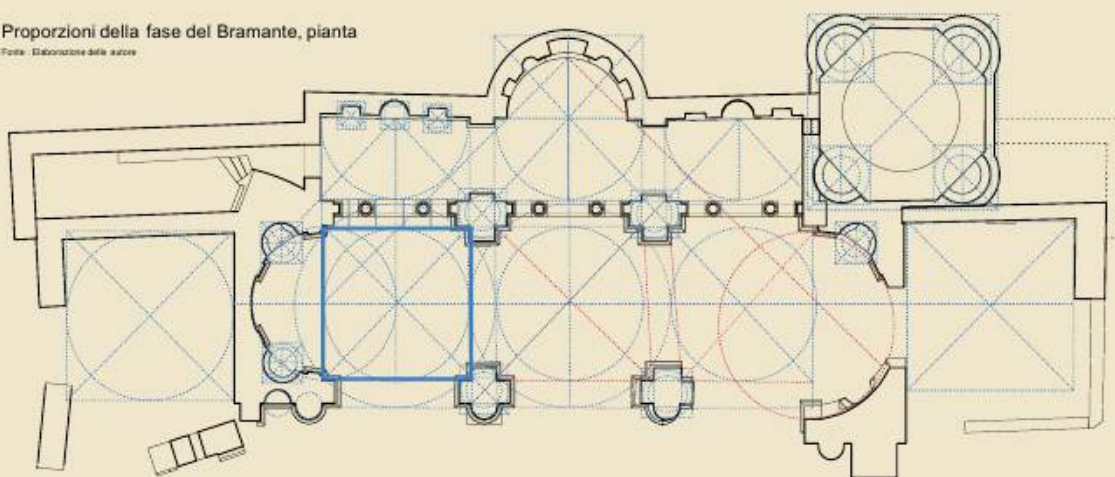


Proporzioni della fase de Giovanni Mangone , pianta

Fonte: Elaborazione dell'autore

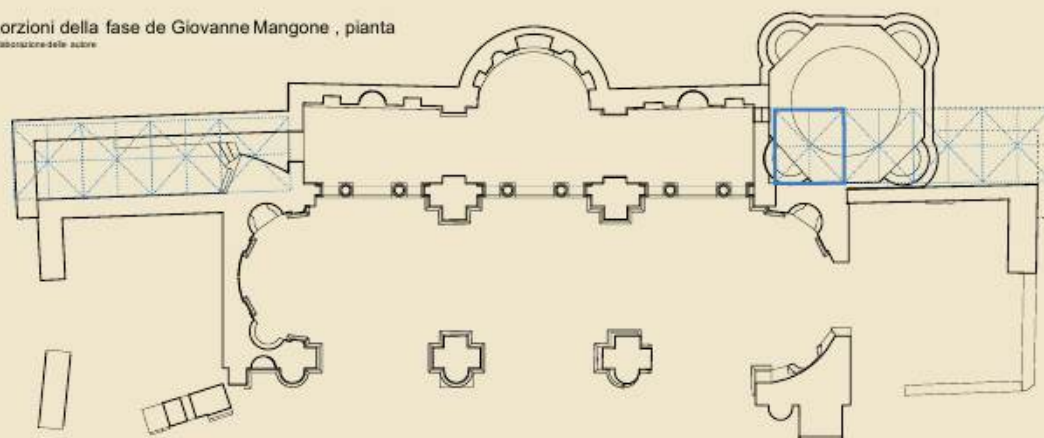


Proporzioni della fase Bramante, prospetto

Fonte: Elaborazione dell'autore

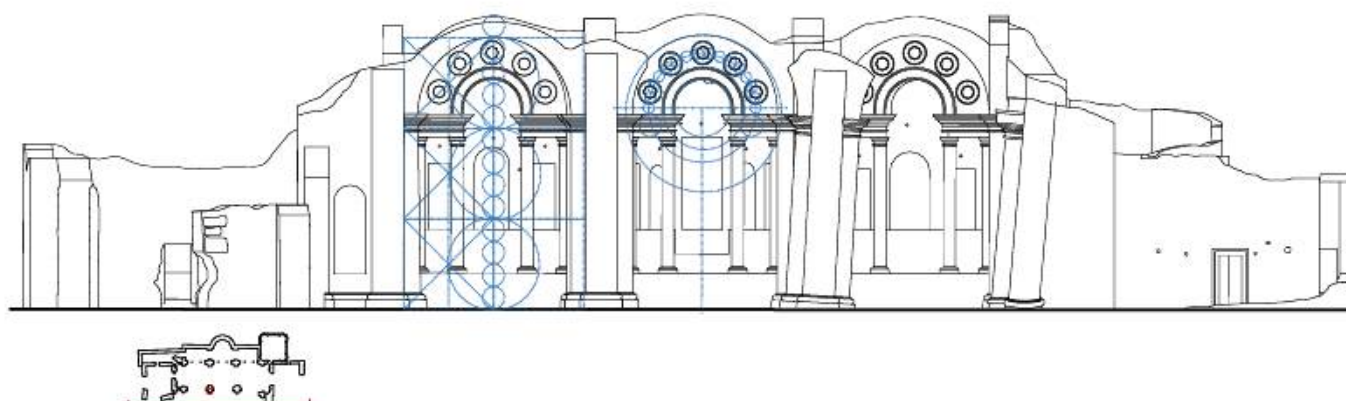

Prospetto SUD

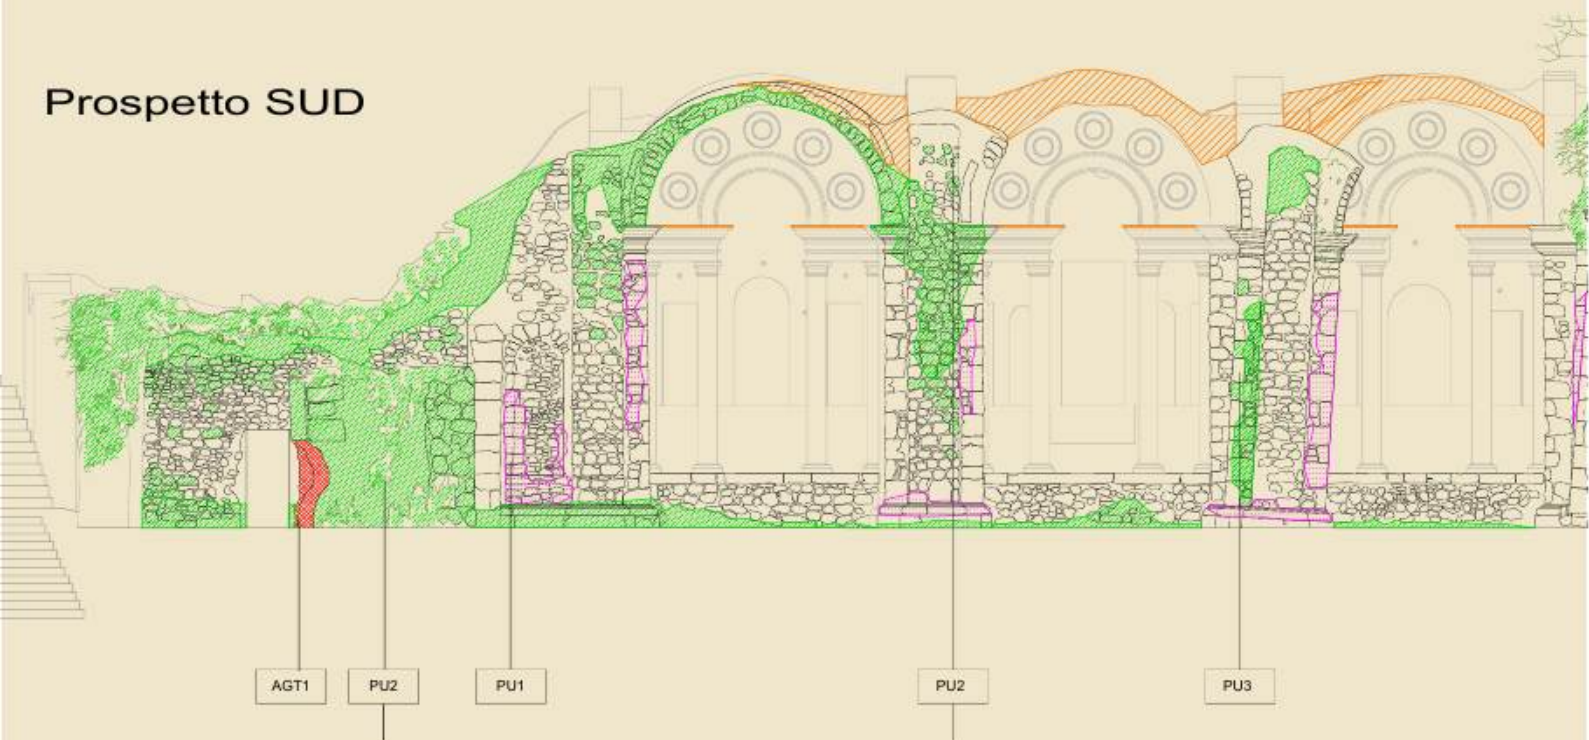

PU1	Pulizia delle superfici con acqua nebulizzata, tenendo conto del principio brandiano della patina come segno del passaggio del tempo.	AS3	Applicazione di sostanze protettive per controllare la flora su superfici asciutte.
PU2	Rimozione delle piante infestanti con strumenti manuali, comprese le radici, e successiva applicazione di prodotti biocidi, prestando attenzione alla muratura.	CO1	Aumento del muro di fondazione per superare i problemi statici che l'organismo architettonico presenta attualmente.
PU3	Pulizia di tutte le superfici trattate ed eliminazione di eventuali residui.	CO2	Operazioni di cucitura e disconnessione nelle parti danneggiate della muratura, utilizzando materiali compatibili e assicurando che le nuove interventi siano riconoscibili.
AS1	Estrazione dei sali solubili tramite l'applicazione di impacchi di argilla assorbente e lavaggio con acqua demineralizzata.	CO3	Iniezioni a pressione controllata di malta compatibile con quella esistente tra i vari stili murari.
AS2	Disinfestazione dalle colonie biologiche sulle superfici tramite l'applicazione di un prodotto biocida, successiva spazzolatura e lavaggio con acqua demineralizzata.	AGT1	Eliminazione degli elementi friabili con utensili morbidi e riempimento della lacuna con una malta reversibile e un materiale compatibile.




SEMESTRES 7et8

LABORATORIO DI RESTAURO

Studio Daniela Esposito, Valeria Montanari

UNIVERSITA LA SAPIENZA, ROMA

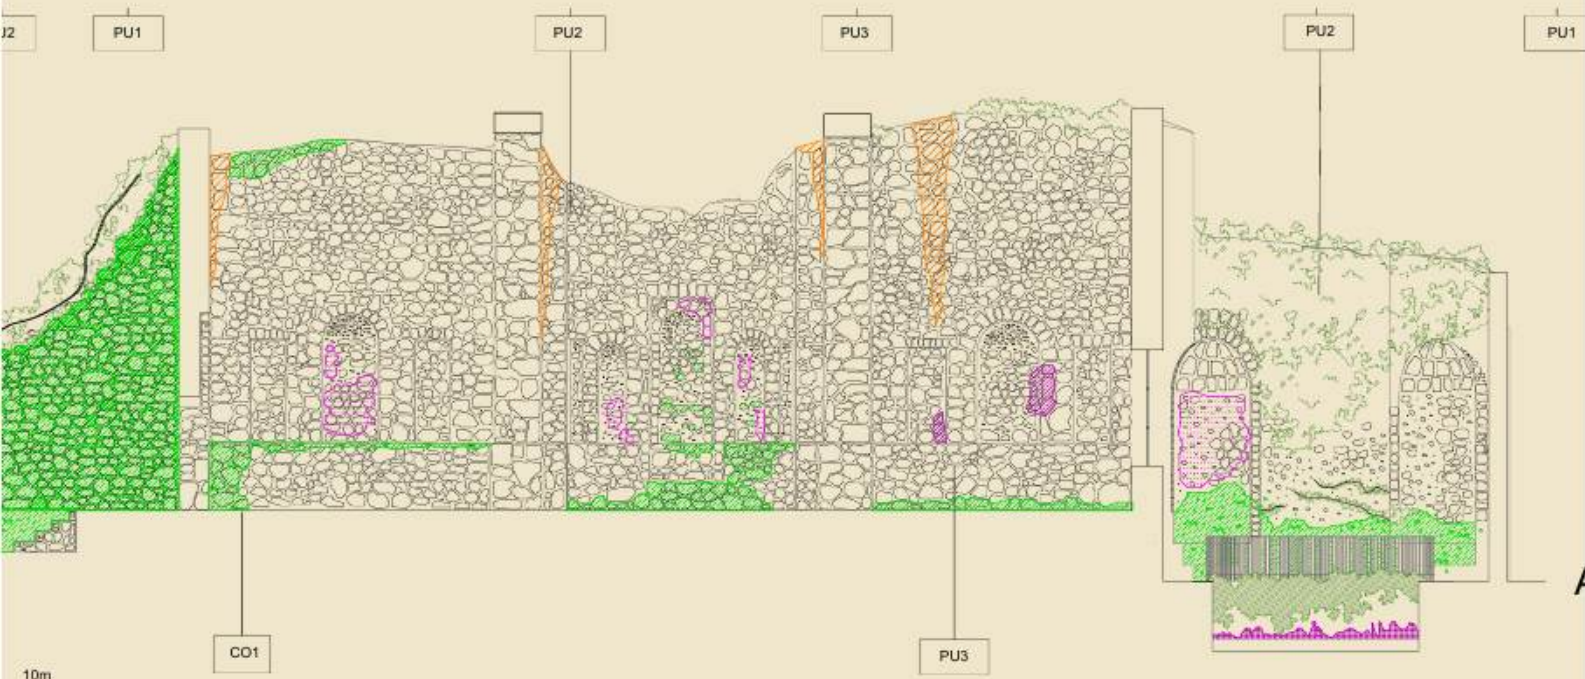

PU1	Pulizia delle superfici con acqua nebulizzata, tenendo conto del principio brandiano della patina come segno del passaggio del tempo.	AS3	Applicazione di sostanze protettive per controllare la flora su superfici asciutte.
PU2	Rimozione delle piante infestanti con strumenti manuali, comprese le radici, e successiva applicazione di prodotti biocidi, prestando attenzione alla muratura.	CO1	Aumento del muro di fondazione per superare i problemi statici che l'organismo architettonico presenta attualmente.
PU3	Pulizia di tutte le superfici trattate ed eliminazione di eventuali residui.	CO2	Operazioni di cucitura e disconnessione nelle parti danneggiate della muratura, utilizzando materiali compatibili e assicurando che le nuove interventi siano riconoscibili.
AS1	Estrazione dei sali solubili tramite l'applicazione di impacchi di argilla assorbente e lavaggio con acqua demineralizzata.	CO3	Iniezioni a pressione controllata di malta compatibile con quella esistente tra i vari stili murari.
AS2	Disinfestazione dalle colonie biologiche sulle superfici tramite l'applicazione di un prodotto biocida, successiva spazzolatura e lavaggio con acqua demineralizzata.	AGT1	Eliminazione degli elementi friabili con utensili morbidi e riempimento della lacuna con una malta reversibile e un materiale compatibile.



SEMESTRES 7et8

LABORATORIO DI RESTAURO

Studio Daniela Esposito, Valeria Montanari

UNIVERSITA LA SAPIENZA, ROMA



IL NINFEO DI BRAMANTE

Projet de restauration de ruines remarquables, celle du ninfée de Bramante à Génazzano, Latium. Ce studio d'un an pendant mon Erasmus fut bouleversant. L'université de la Sapienza à Rome, possède une méthode particulière de faire projet.

Il s'agit de faire une analyse du site d'une manière très approfondie. Avant d'imaginer un projet il faut impérativement étudier toutes les caractéristiques du lieu, son histoire d'abord, puis sa géographie sous plusieurs échelles. La philologie, la pluviométrie, la lithographie. Même à l'échelle du matériau, des joints entre les pierres nous analysons les couleurs, les textures pour identifier leurs compositions chimiques.


SEMESTRE 9
STUDIO,
JARDIN
PERMACULTUREL
Philippe Villen



Maquette tranche du projet de jardins perma-culturels sur site : les extérieurs de L'ENSAPB. Plusieurs espaces usages ont été envisagés ainsi qu'une proposition de « phasage temporel » respectant des estimations budgétaire. Le projet se veut participatif, avec une ligne directrice claire : UNE MISE EN ŒUVRE SIMPLE.



Une réflexion axée sur des architectures éphémères, le réemploi des chutes de nos ateliers maquette et bois principalement. La nature saccadée de notre site nous a inspiré une diversité de micro climats. Le fait de choisir un site que l'ont connaissait et fréquentait quotidiennement nous a permis de d'imaginer une réelle projection : Que serait-il de fréquenter ces lieux dans Paris en 2070? L'école comme Oasis, refuge climatique ouvert à tous·tes.

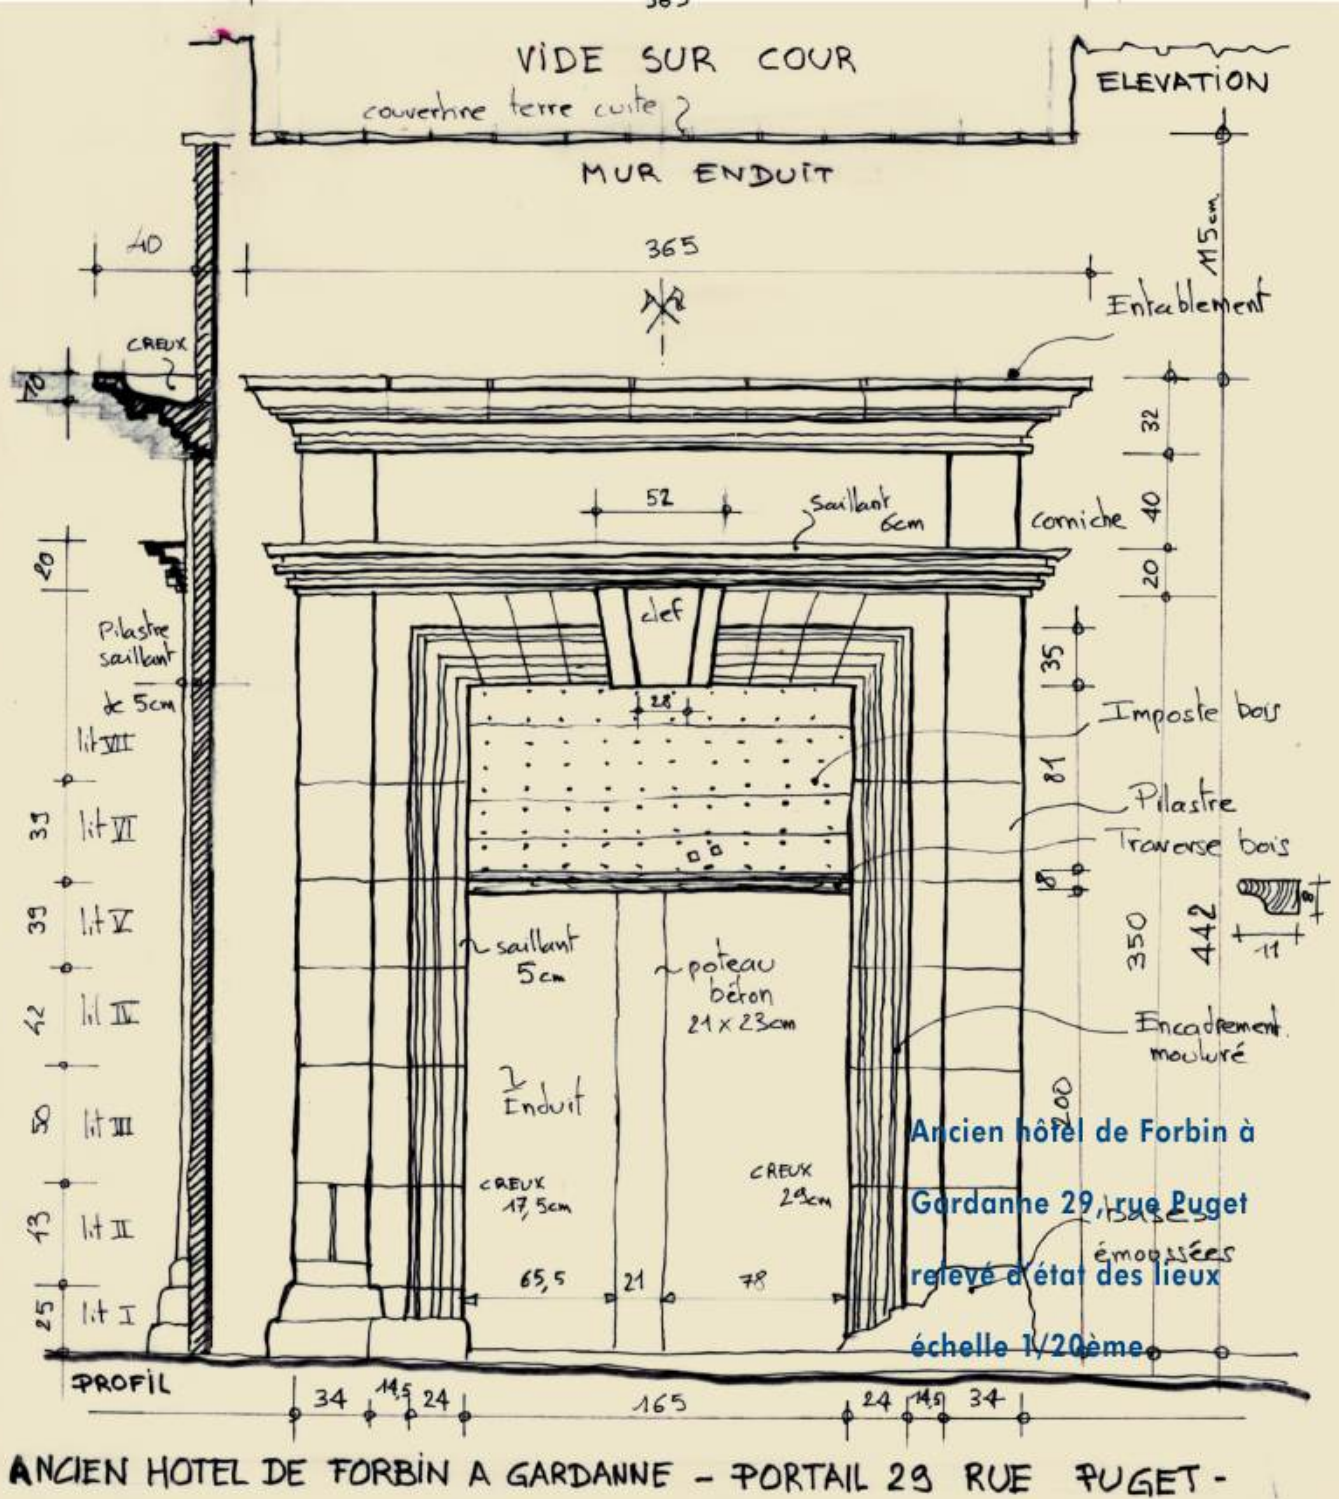

STAGE

ANIS Architecture Jérôme Durand,
Architecte du Patrimoine Juin 2023



Création d'une devanture
de magasin, 25 rue
Monclar, 13100 Aix en
Provence.

Photographie de
l'ancienne devanture d'un
CIC.

STAGE

ANIS Architecture Jérôme Durand,
Architecte du Patrimoine Juin 2023



Opération:
Creation d'une devanture
25, Rue Mondlar
13100 Aix-en-Provence

Document:
**Devanture
PROJET**

Phase:
PROJET

Maitrise d'ouvrage:
Novoid plus
4 rue des chaudronniers
13100 Aix en Provence

Date:
12/06/2023
Echelle:
1:50e

Architecte:
Jérôme Durand Architecte
1, rue Lacépède
13100 Aix-en-Provence
T 06 03 90 39 31

ANIS
Architecture

STAGE

ANIS Architecture Jérôme Durand,
Architecte du Patrimoine Juin 2023



Création d'une devanture
de magasin, 25 rue
Monclar, 13100 Aix en
Provence.


Photographie post-projet.






ARTS PLASTIQUES

Boîtes en carton dessin à la plume, L2

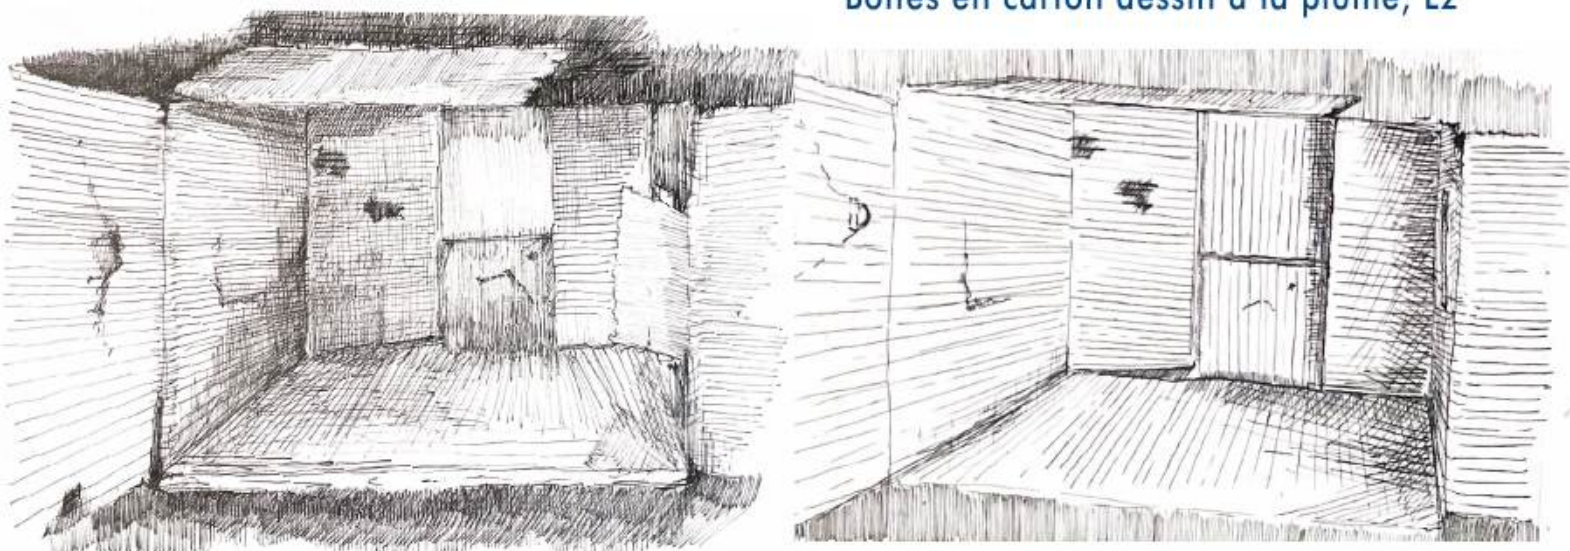

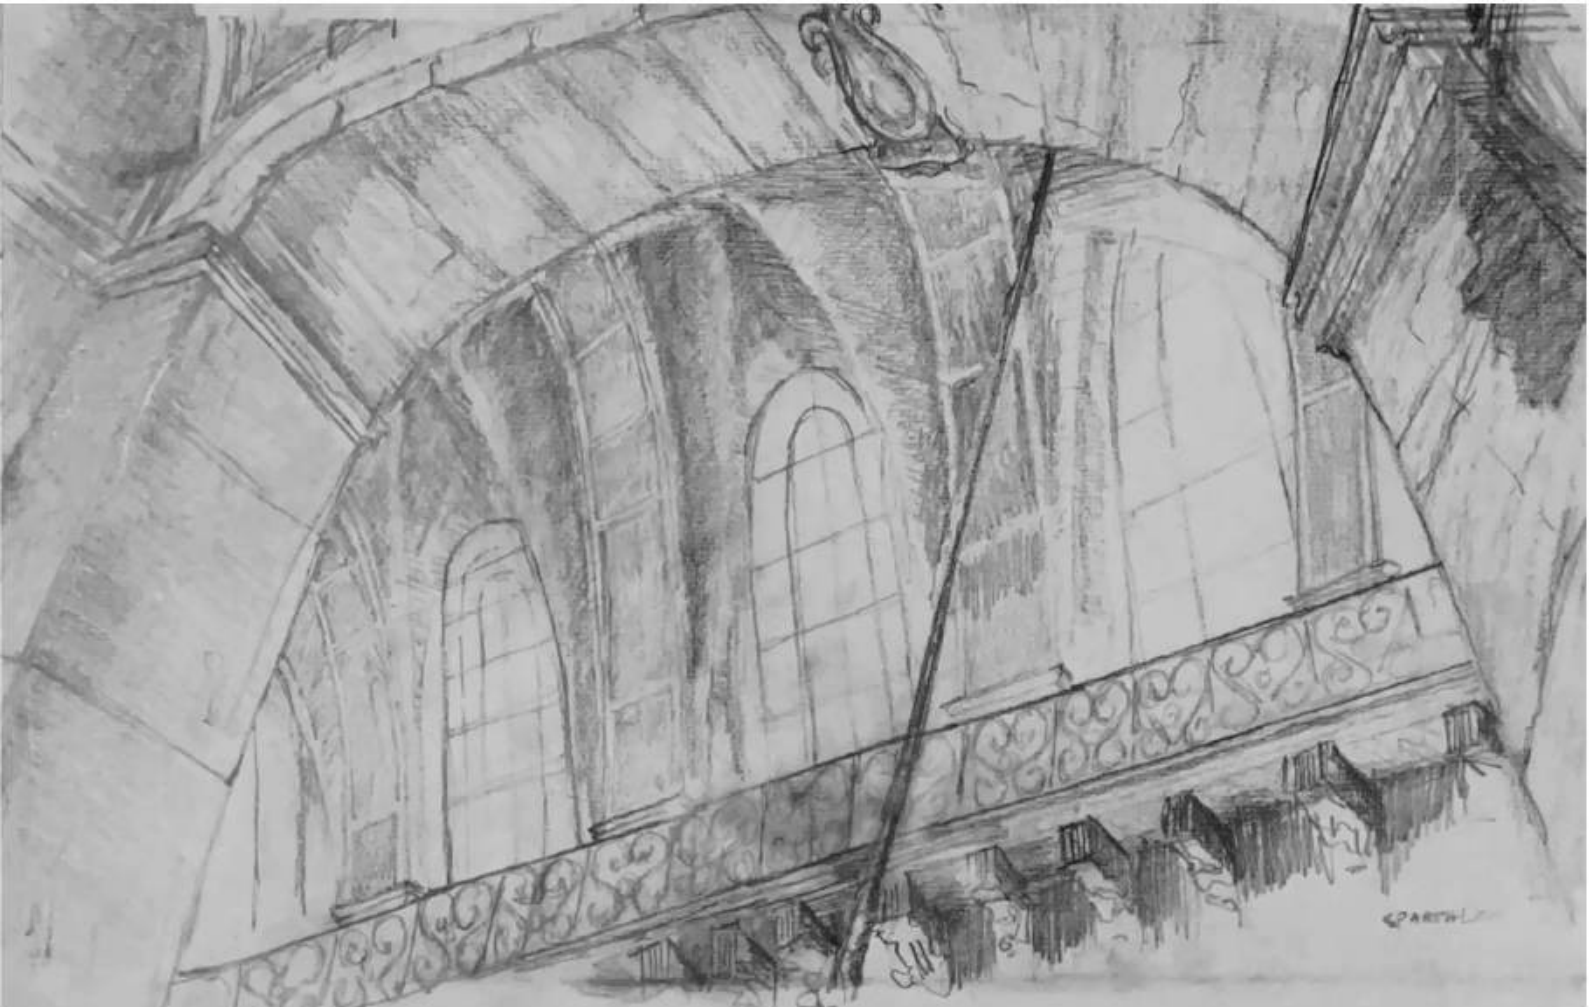

Paroisse Saint Nicolas des champs, L2



Terrasse des Galeries Lafayette, L2




Voyage d'arts
Plastiques L2 Italie
du Nord. Rue et
Cloître du cimetière
De Ferrare.






Voyage d'arts
Plastiques L2 Italie
du Nord.
Musée archéologique
Arcades, plume

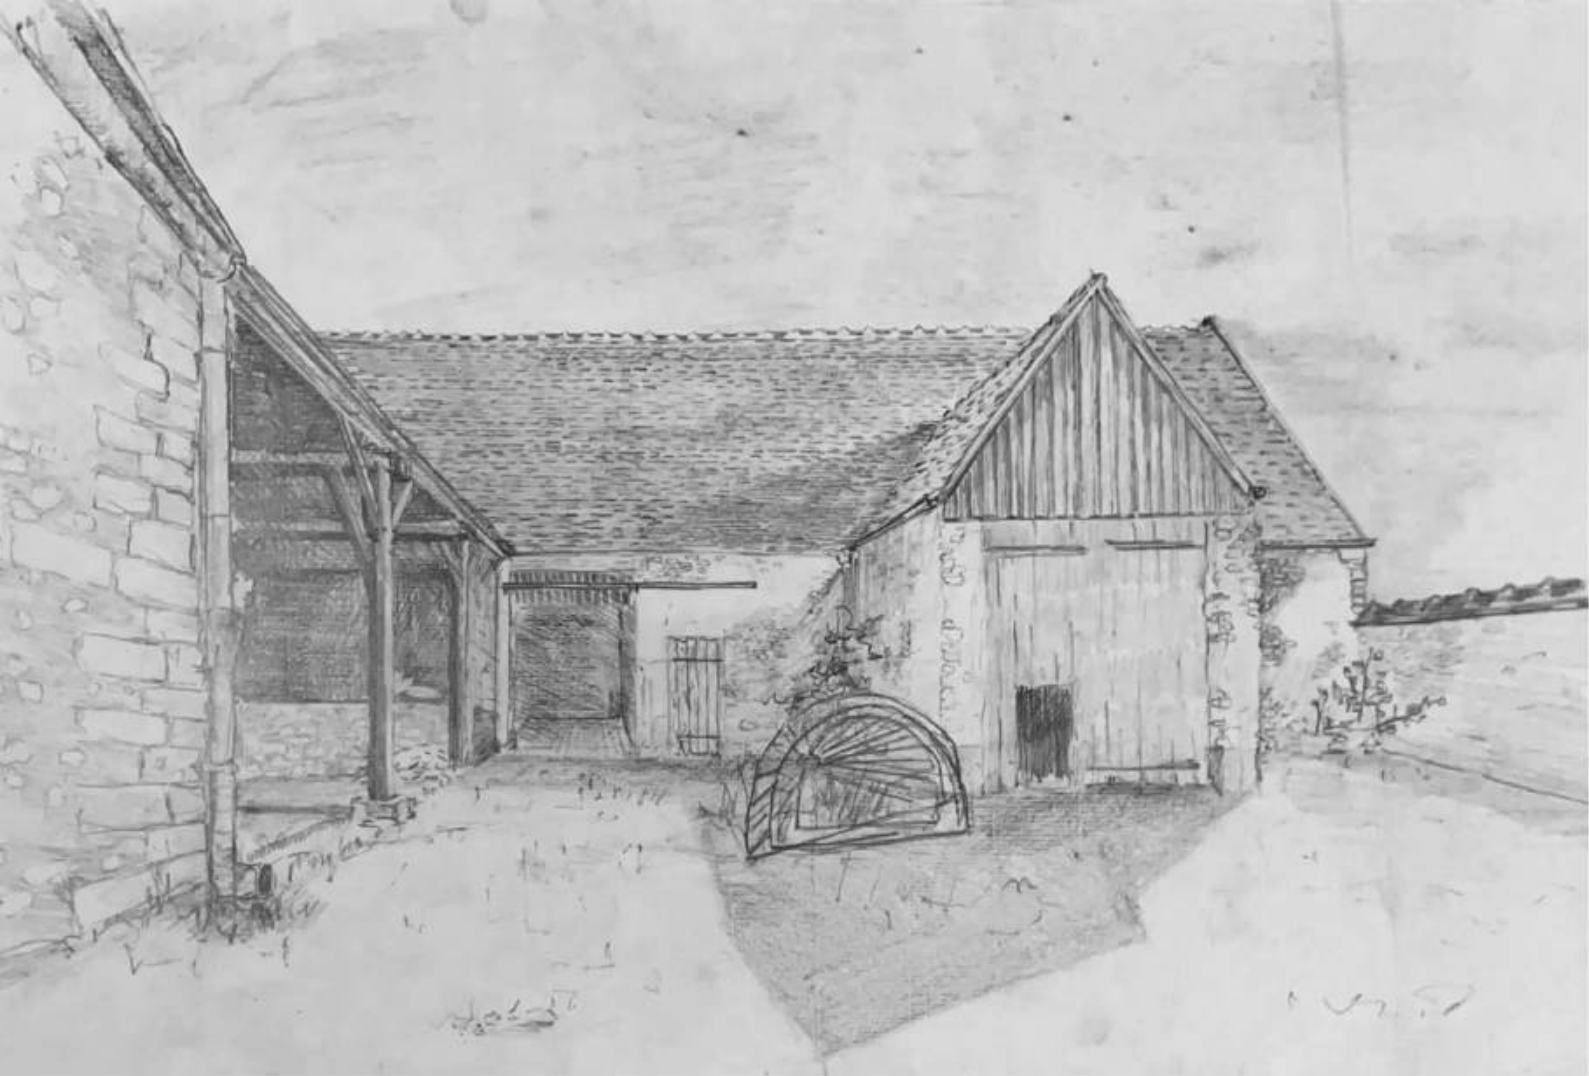


Ferme de la Croix Blanche (vue depuis la Cours) Crayons graphite sur papier, L3.

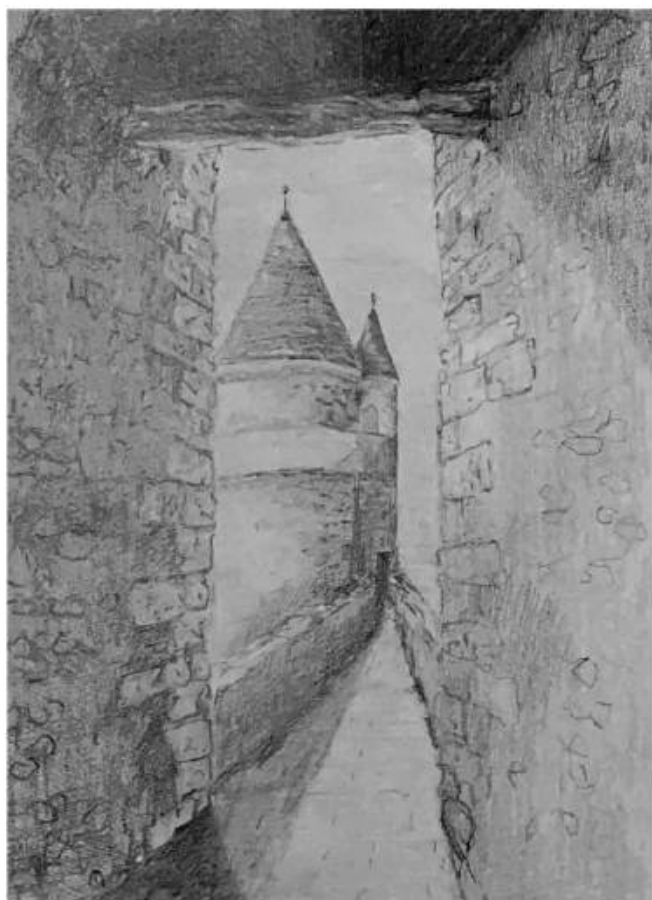



1^{er} Dessin pour eau forte, Cimetière du Père Lachaise , L3

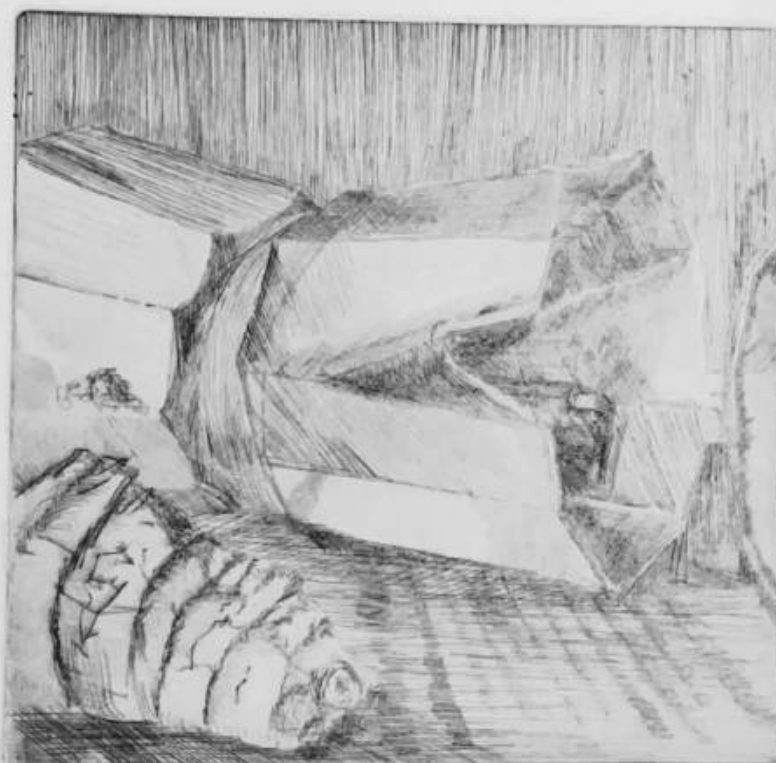

Nature morte, Gravure sur zinc, pointe sèche , L3